


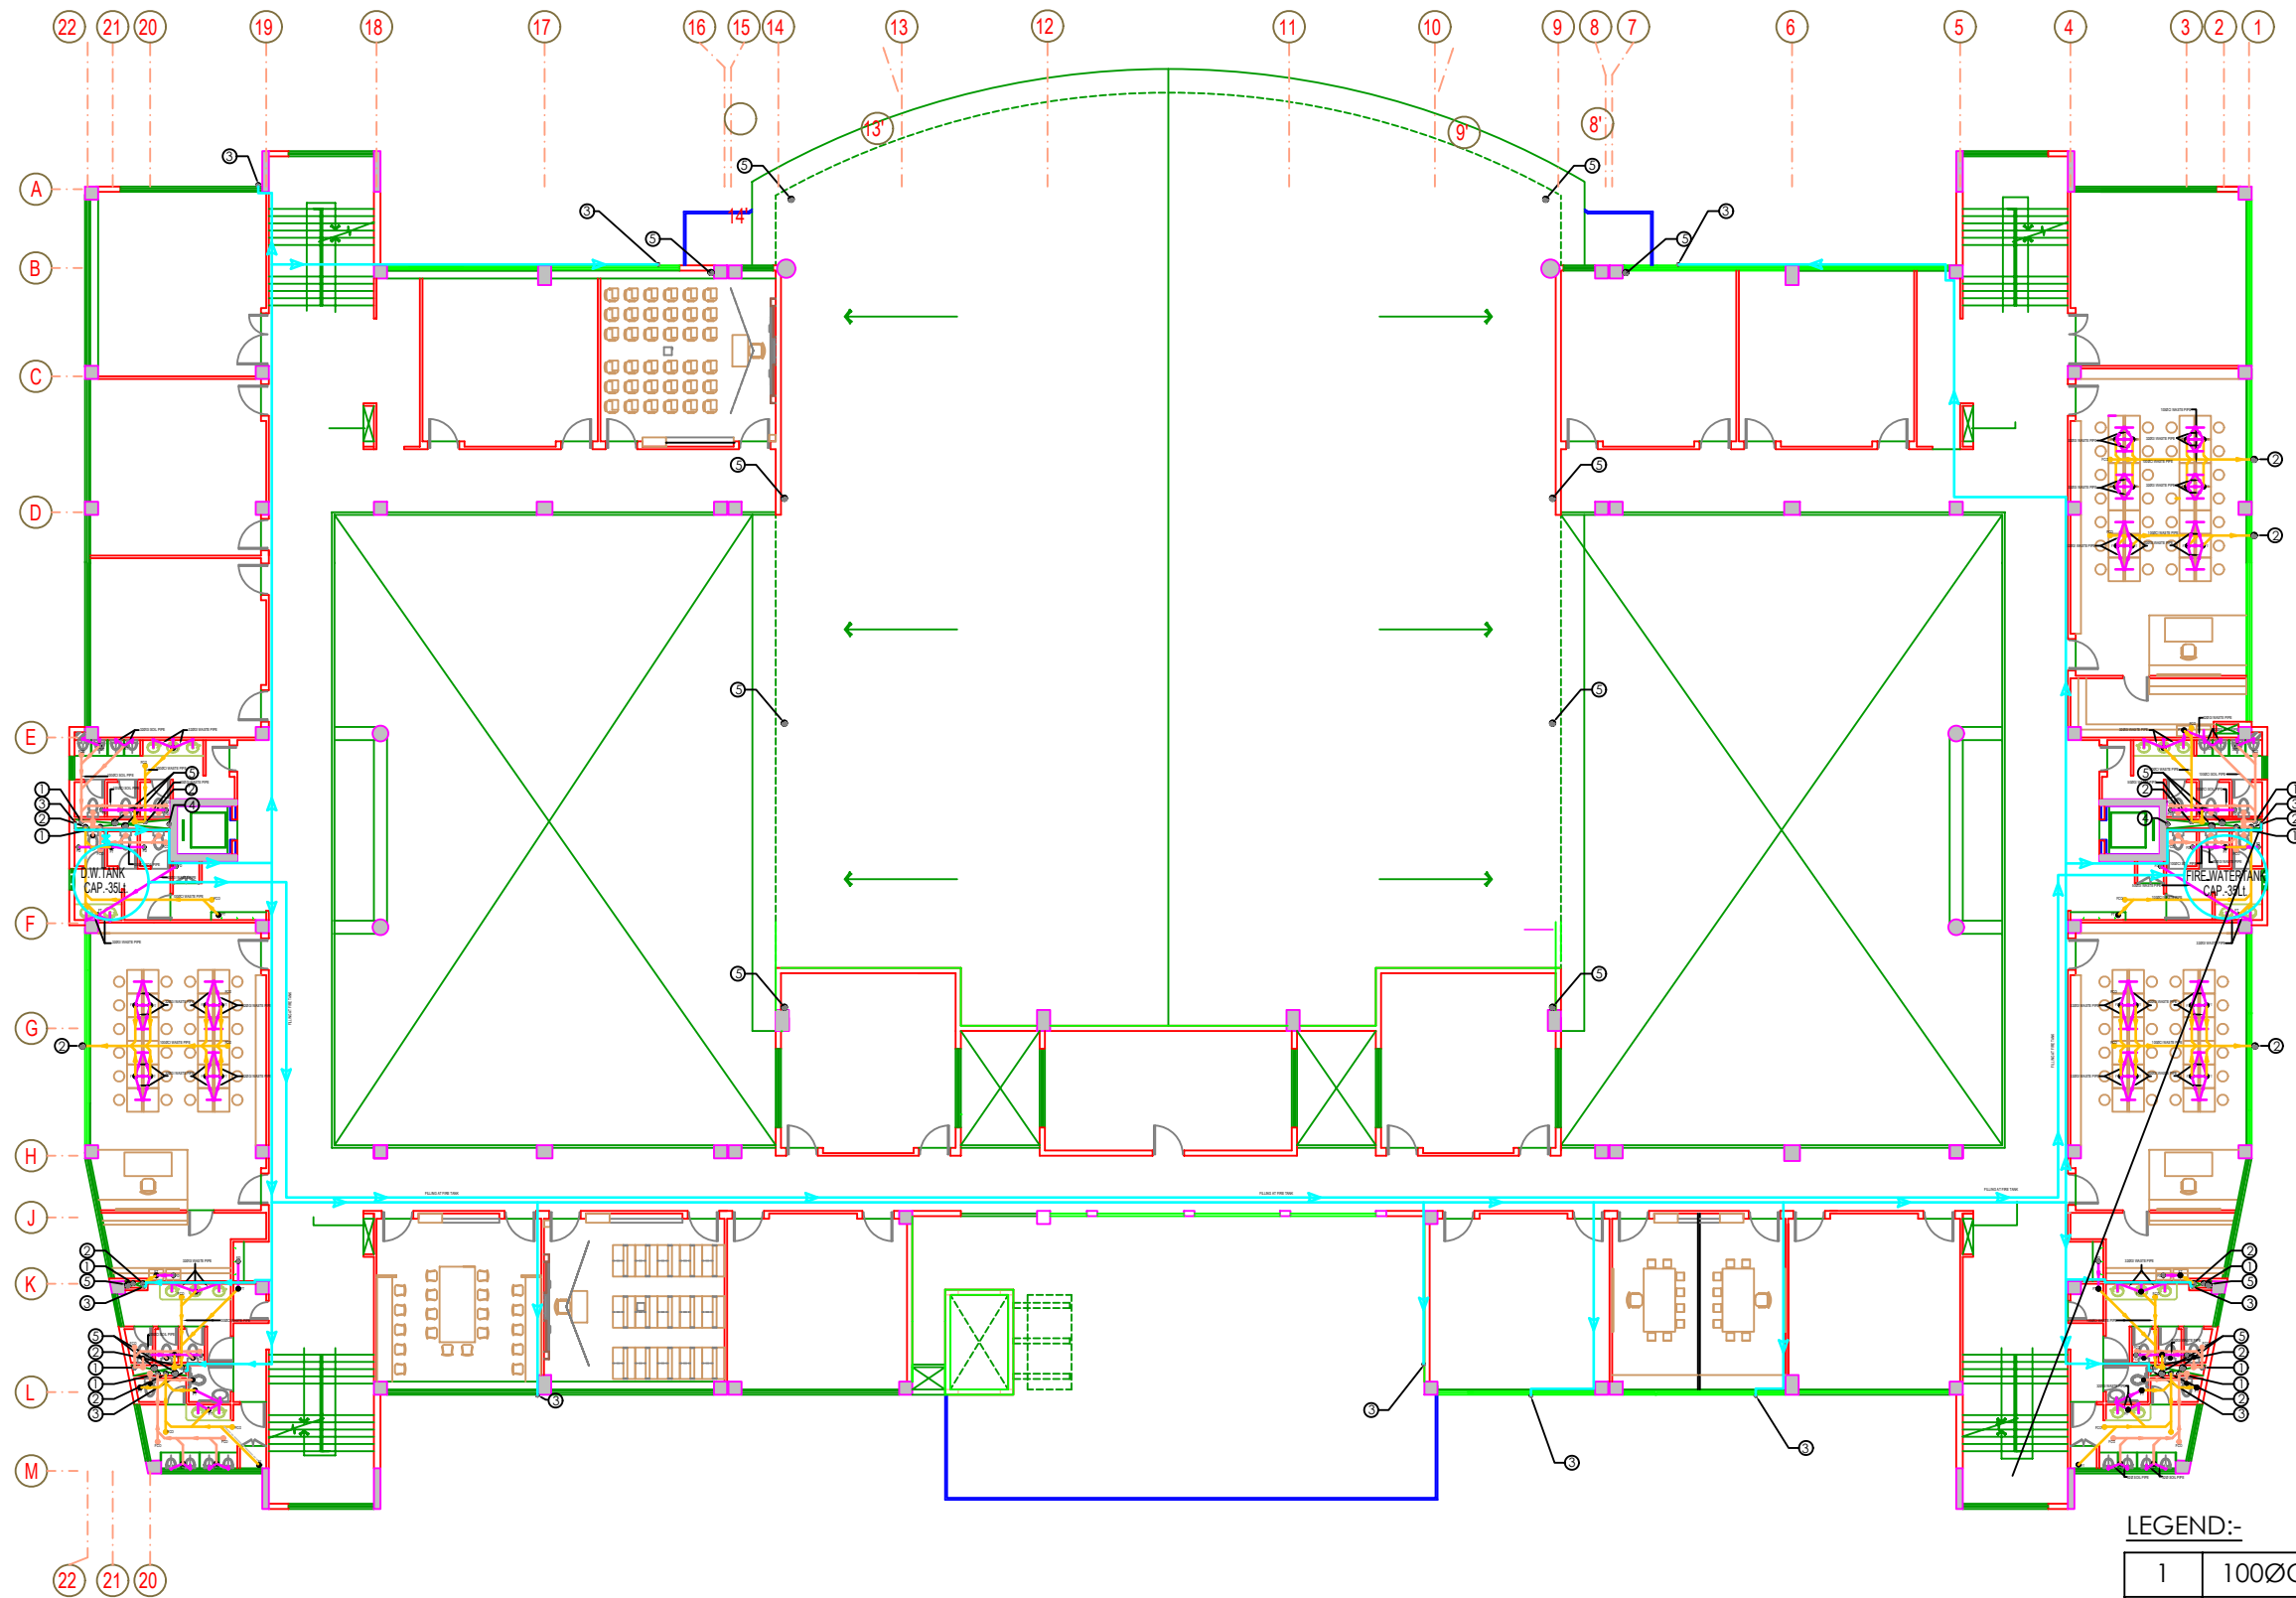

LEGEND:-

1	100ØC.I. SOIL & VENT PIPE
2	100ØC.I. WASTE & VENT PIPE
3	CWS DN.TAKE FROM O.H.TANK
4	CWS RISER TO O.H.TANK
5	150ØC.I. RAIN WATER PIPE
1a	100ØC.I. VENT PIPE

IS THE PROPERTY OF ABIN DESIGN STUDIO AND CANNOT BE COPIED, CIRCULATED OR
UNNER OTHER THAN THE PURPOSE FOR WHICH IT IS ISSUED WITHOUT THEIR WRITTEN

JRED DIMENSIONS ONLY

NS ARE TO ROUGH SURFACES OR CENTRE LINES AND DO NOT INCLUDE FINISHES UNLESS
IE

ANCY N DIMENSIONS OR BETWEEN THIS DRAWING & ANY OTHER MUST BE BROUGHT TO
IMEDIATE NOTICE

NS ARE IN MILLIMETERS

DRAWN	R.S.R	RELEASED FOR
CHECKED	B.K.NAUTIYAL	CONCEPT
DATE	JAN-2008	APPROVAL
FILENAME	D:\CLIENTS\SOUTH CITY\SCHOOL\MAILED- 01.11.07\S THIRD FLOOR PLAN 20.09.08	PRELIMINARY
SCALE	1:200	TENDER
DRAWING NO.:	PL-03	INFORMATION ONLY
		CONSTRUCTION
		AS-BUILT

TITLE: THIRD FLOOR PLAN
SCHOOL BUILDING

PROJECT:
SOUTH CITY
KOLKATA

CONSULTANT:

Deolalikar
Consultants Pvt. Ltd.

Plumbing and Fire Fighting System Consultant
A-1/152 Nebsari, IGNOU Road
New Delhi - 110068, India
Ph.: 011 - 41297252, 41297253
011 - 32646999, 32635999
Fax: -


NORTH



ARCHITECTS:

ABIN DESIGN STUDIO

ARCHITECTURE INTERIOR DESIGN GRAPHICS INDUSTRIAL DESIGN
74 G, BONDEL ROAD, GROUND FLOOR, KOLKATA - 700 019

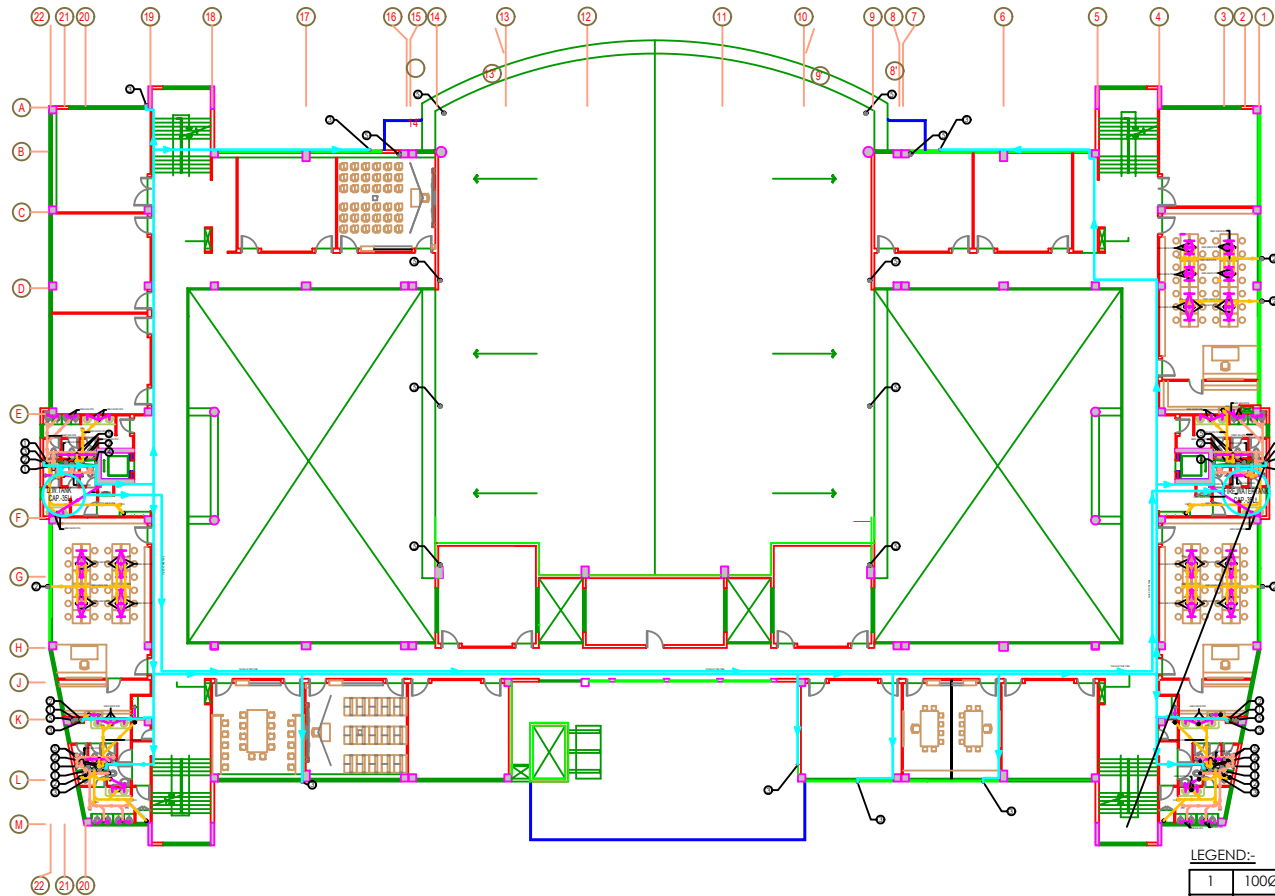

LEGEND:-

1	100ØC.I. SOIL & VENT PIPE
2	100ØC.I. WASTE & VENT PIPE
3	CWS DN.TAKE FROM O.H.TANK
4	CWS RISER TO O.H.TANK
5	150ØC.I. RAIN WATER PIPE
1a	100ØC.I. VENT PIPE

NOTES

- THIS DRAWING IS THE PROPERTY OF ABN DESIGN STUDIO AND CANNOT BE COPIED, CIRCULATED OR USED IN ANY MANNER OTHER THAN THE PURPOSE FOR WHICH IT IS ISSUED WITHOUT THE WRITTEN PERMISSION.
- WORK TO BE DONE DIMENSIONS ONLY.
- ALL DIMENSIONS ARE TO FINISH SURFACES OF CURVE LINES AND DO NOT INCLUDE FINISHES UNLESS NOTED OTHERWISE.
- ANY DISCREPANCY IN DIMENSIONS OR BETWEEN THIS DRAWING & ANY OTHER MUST BE BROUGHT TO ARCHITECT'S IMMEDIATE NOTICE.
- ALL DIMENSIONS ARE IN MILLIMETERS.

DRAWN	R.S.R.	RELEASED FOR
CHECKED	B.K.NAUTIAL	CONCEPT
DATE	JAN-2008	APPROVAL
FILENAME		PRELIMINARY
		TENDER
		INFORMATION ONLY
SCALE	1:200	CONSTRUCTION
DRAWING NO.:	PL-03	AS-BUILT

TITLE: THIRD FLOOR PLAN
SCHOOL BUILDING

PROJECT:
SOUTH CITY
KOLKATA

CONSULTANT:

Deolalikar Consultants Pvt. Ltd.
Surveying and Fire Fighting System Consultant
A-17/12, Nehru Park, 62ND Road,
New Delhi - 110068, India
Ph.: 011-41297252, 41297253
011-32646999, 32635999
Fax: -

NORTH



ARCHITECTS:

ABN DESIGN STUDIO
ARCHITECTURE INTERIOR DESIGN GRAPHICS INDUSTRIAL DESIGN
74 G. BONDEL ROAD, GROUND FLOOR, KOLKATA - 700 019