




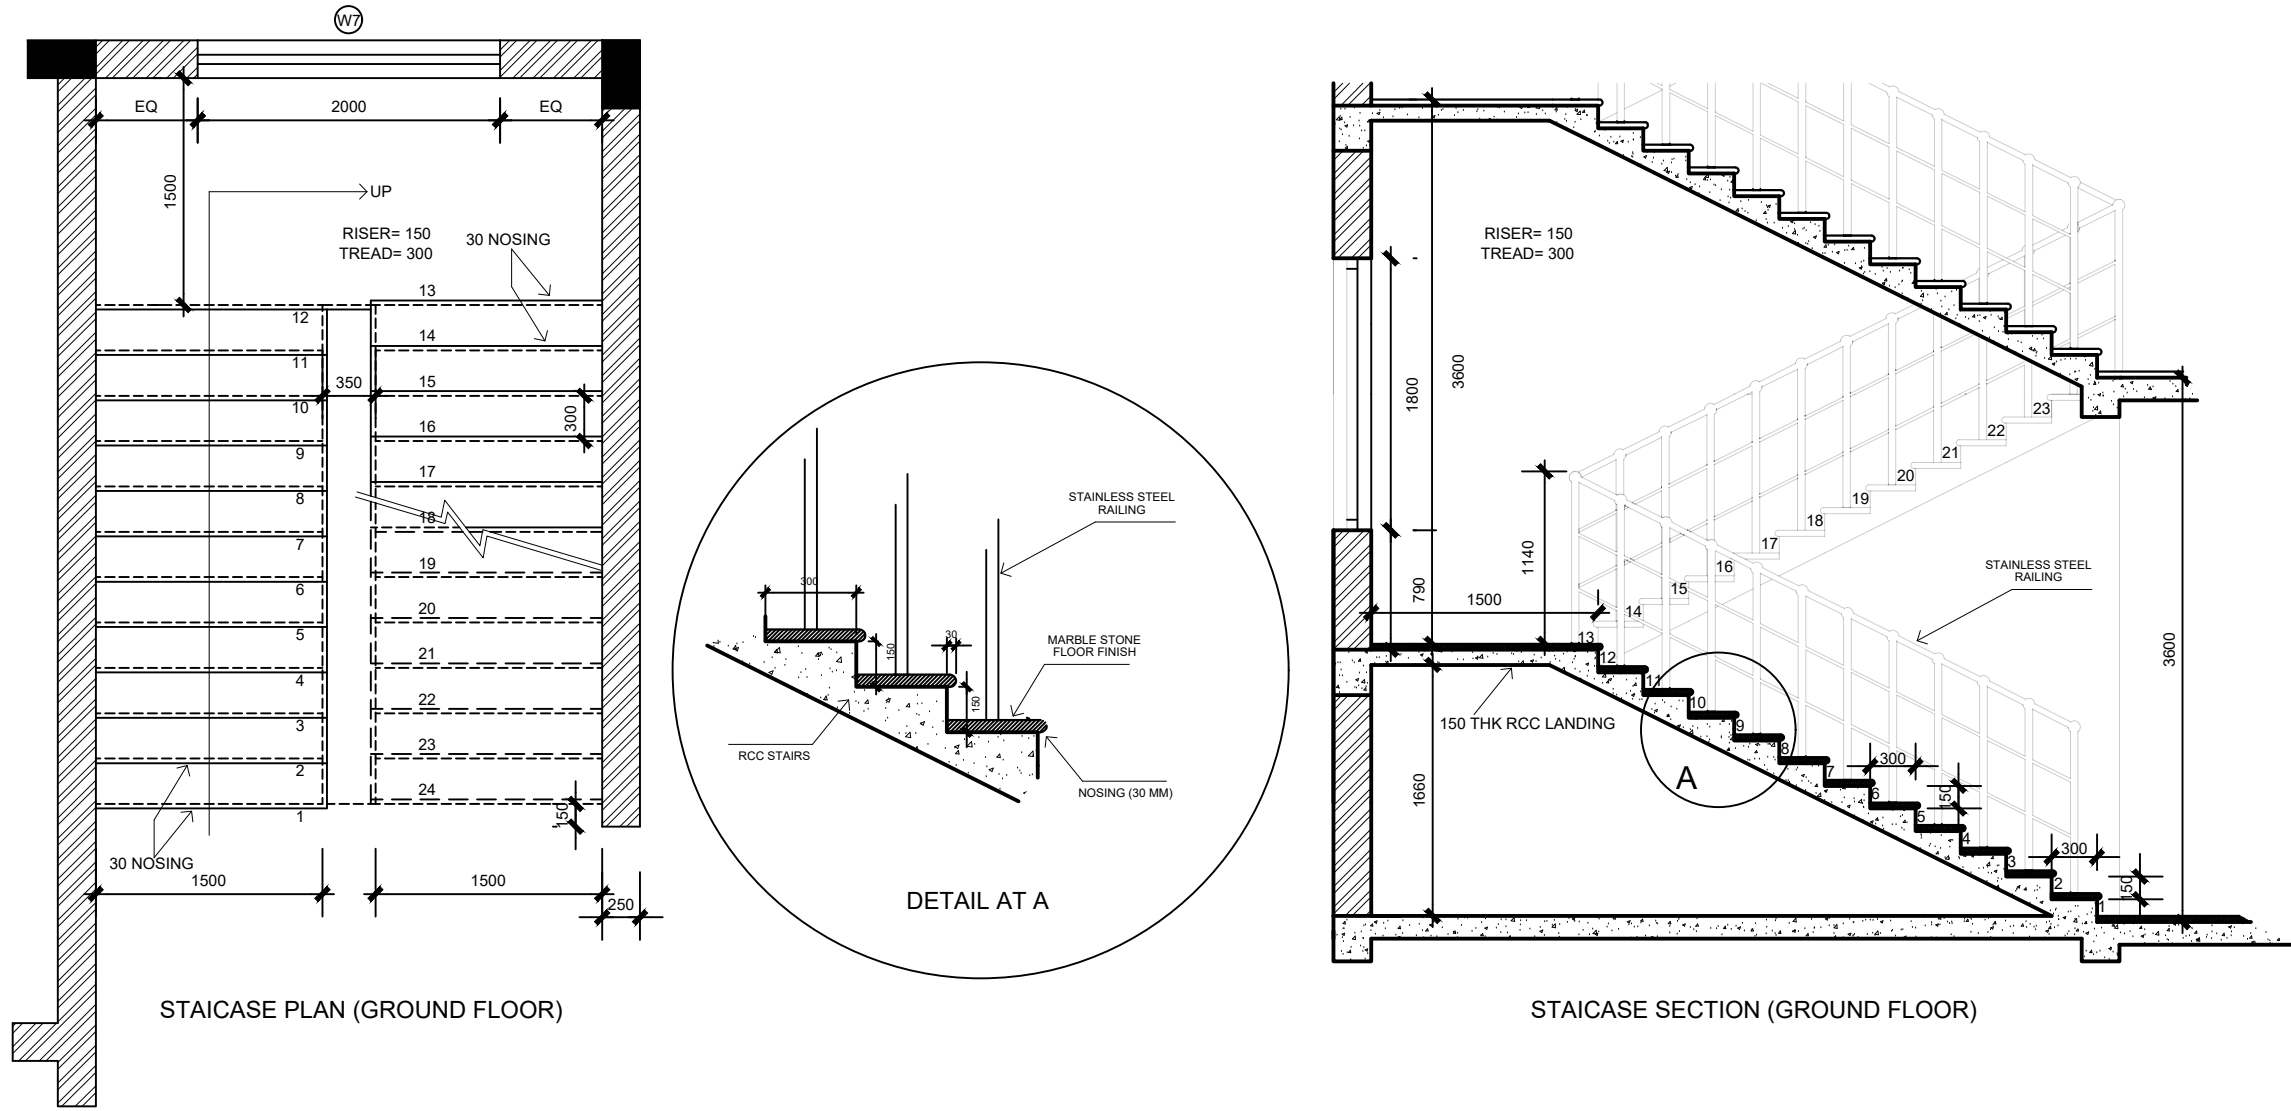


STAIRCASE PLAN (GROUND FLOOR)

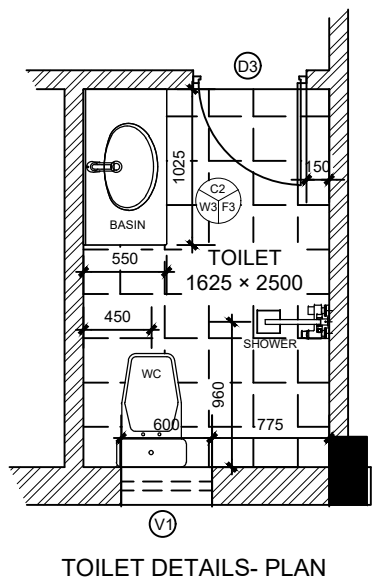

TOILET DETAILS- PLAN

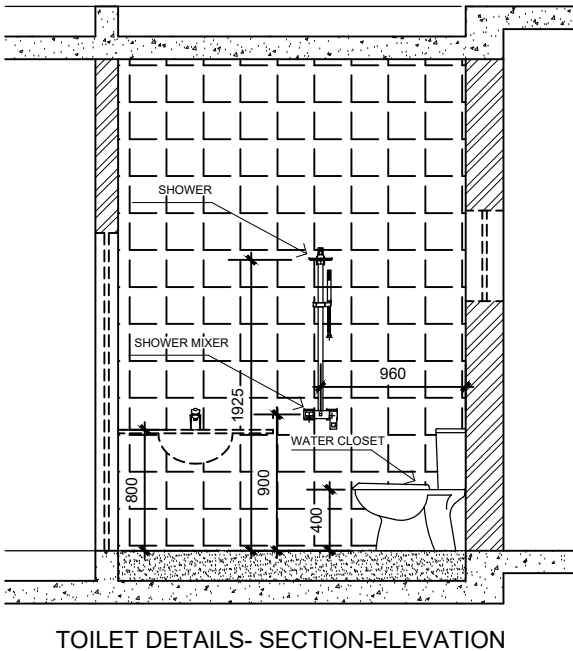

TOILET DETAILS- SECTION-ELEVATION

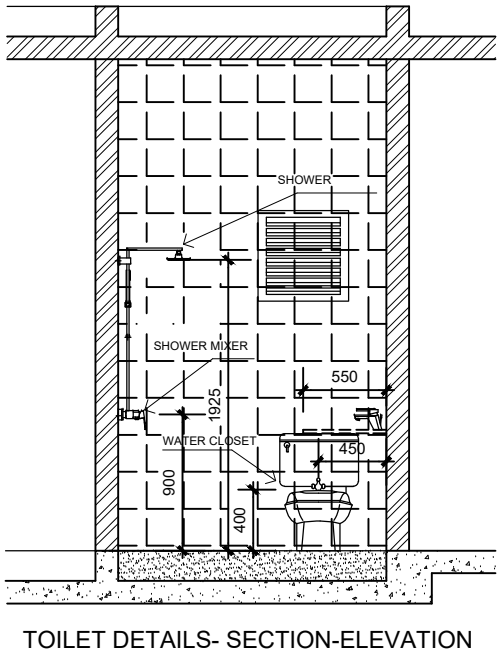

TOILET DETAILS- SECTION-ELEVATION

NOTES

ALL DIMENSIONS ARE IN MM UNLESS NOTED OTHERWISE
THE DIMENSIONS ARE TO BE READ AND NOT SCALED OFF THE DRAWING.
ANY DISCREPENCY IN THE DRAWING SHALL BE BROUGHT TO THE NOTICE OF THE ARCHITECTS.
THIS DRAWING IS TO BE READ IN CONJUNCTION WITH OTHER RELEVANT DRAWINGS.

Name: PRAKHAR VERMA
Roll No: 22AR10017

Working Drawing-I (AR32201)
Semester: VI
SPRING-2025

Department of Architecture & Regional Planning
Indian Institute of Technology
Kharagpur

Drawing Title **DETAILING**

Scale - **1:50**

Date- 07/04/2025

Dwg no. 2

