


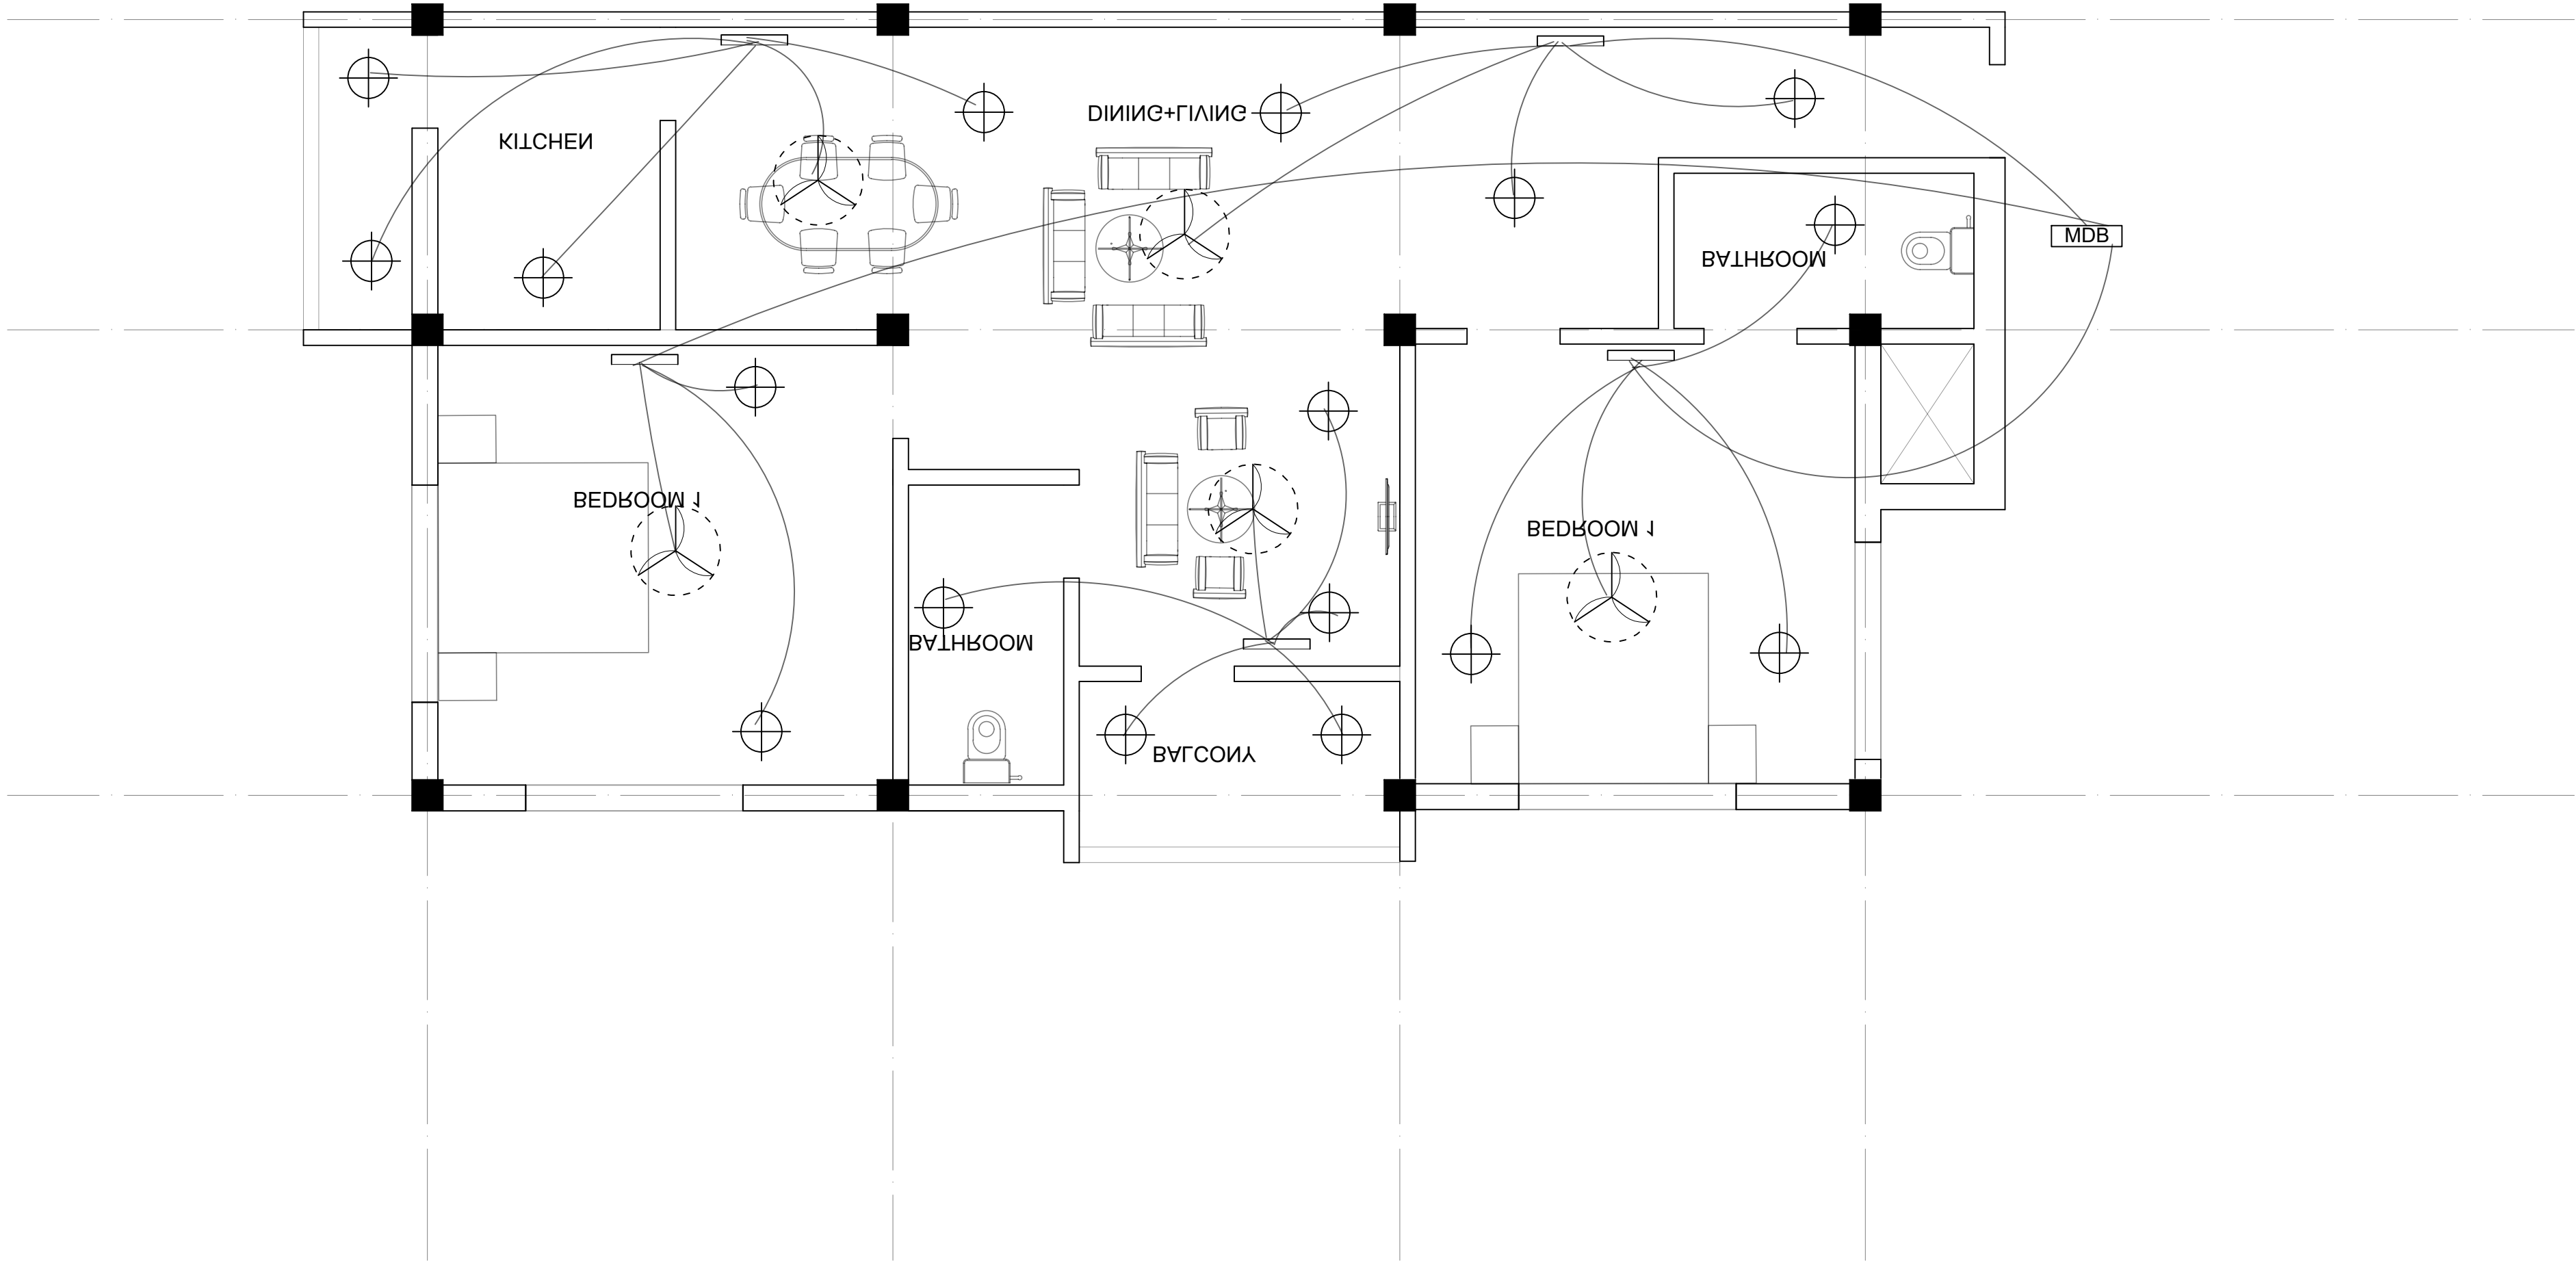

SYMBOL OF ELECTRICAL FIXTURES

LEGEND	
	CEILING LIGHT
	FAN
	EXHAUST FAN
	CHANDELIER
	TUBELIGHT
	WALL MOUNTED LIGHT
	BOARD WITH SWITCHES
	MAIN DISTRIBUTION BOARD
	AC

NOTES

ALL DIMENSIONS ARE IN MM UNLESS NOTED OTHERWISE

THE DIMENSIONS ARE TO BE READ AND NOT SCALED OFF THE DRAWING.

ANY DISCREPENCY IN THE DRAWING SHALL BE BROUGHT TO THE NOTICE OF THE ARCHITECTS.

THIS DRAWING IS TO BE READ IN CONJUNCTION WITH OTHER RELEVANT DRAWINGS.

Name: PRAKHAR VERMA
Roll No: 22AR10017

Working Drawing-I (AR32201)
Semester: VI
SPRING-2025

Department of Architecture & Regional Planning
Indian Institute of Technology
Kharagpur

Drawing Title
ELECTRICAL LAYOUT

Scale -
1:50

Date-
07/04/2025

Dwg no.
2