


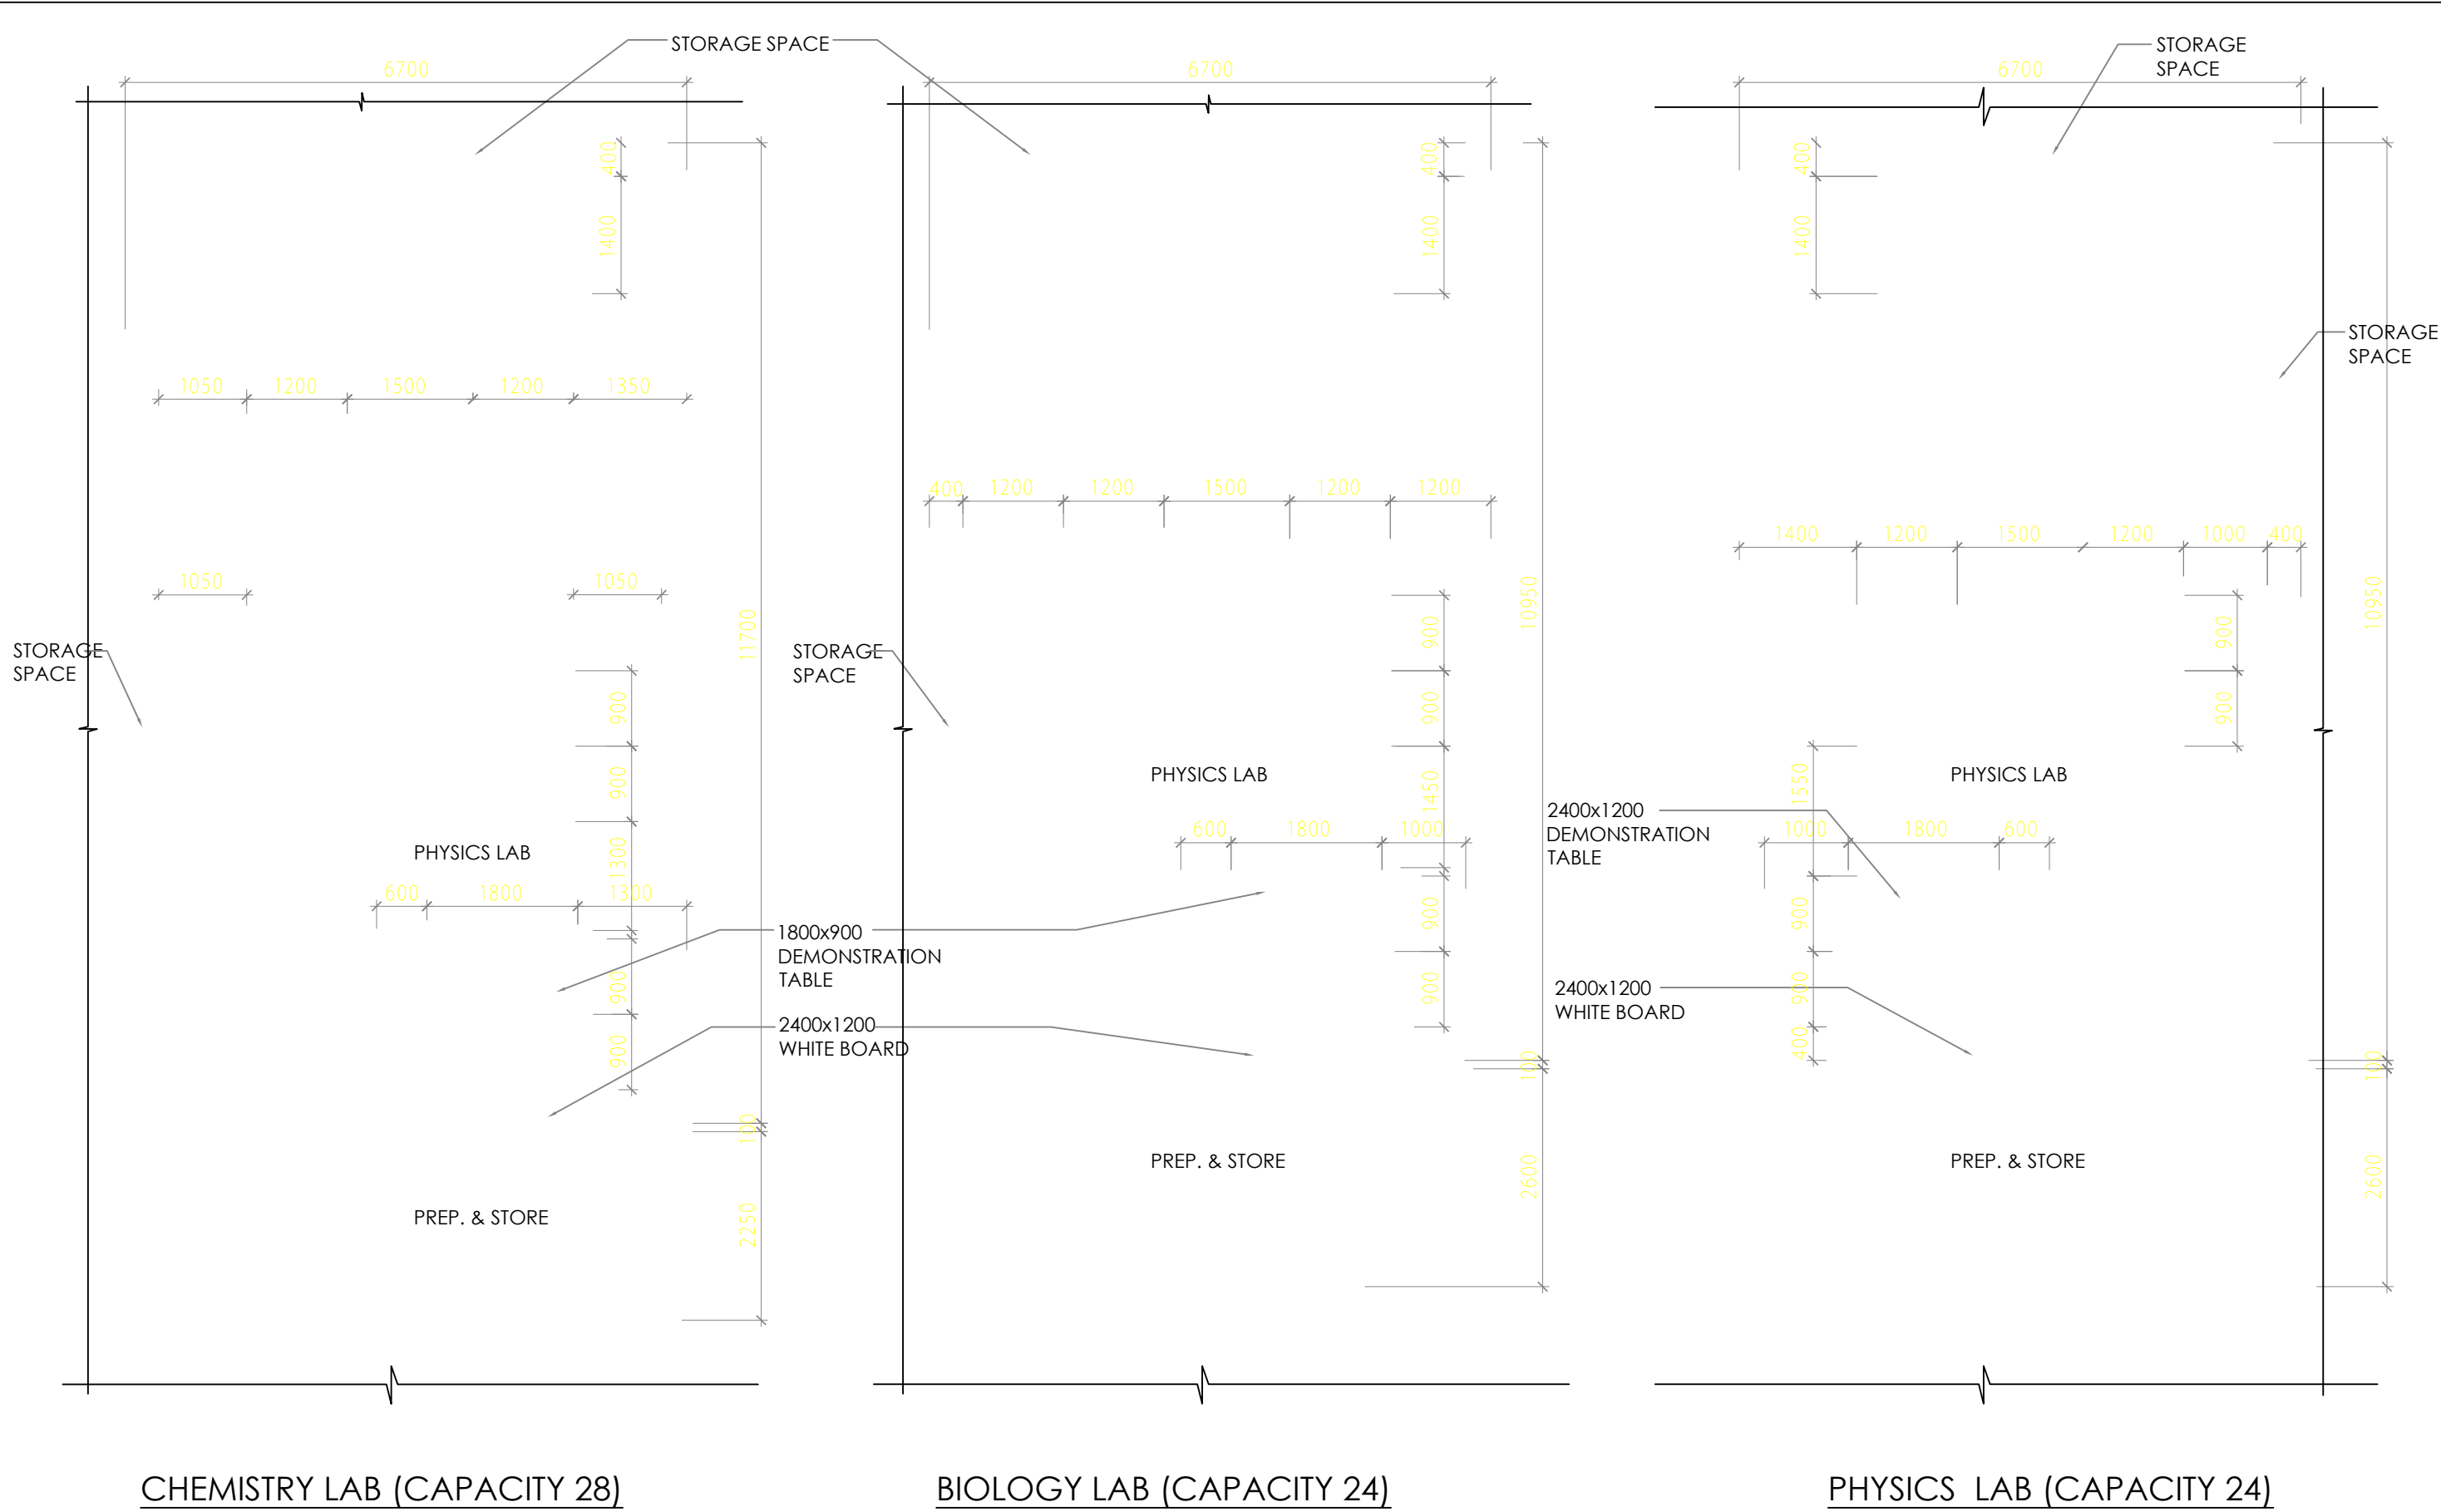


CHEMISTRY LAB (CAPACITY 28)


BIOLOGY LAB (CAPACITY 24)

PHYSICS LAB (CAPACITY 24)


NOTES 1. THIS DRAWING IS THE PROPERTY OF ABIN DESIGN STUDIO AND CANNOT BE COPIED, CIRCULATED OR USED IN ANY MANNER OTHER THAN THE PURPOSE FOR WHICH IT IS ISSUED WITHOUT THEIR WRITTEN PERMISSION 2. WORK TO FIGURED DIMENSIONS ONLY 3. ALL DIMENSIONS ARE TO ROUGH SURFACES OR CENTRE LINES AND DO NOT INCLUDE FINISHES UNLESS NOTED OTHERWISE 4. ANY DISCREPANCY IN DIMENSIONS OR BETWEEN THIS DRAWING & ANY OTHER MUST BE BROUGHT TO ARCHITECT'S IMMEDIATE NOTICE 5. ALL DIMENSIONS ARE IN MILLIMETERS	DRAWN		RELEASED FOR		TITLE: INTERIOR LAYOUT PROJECT: SOUTH CITY INTERNATIONAL SCHOOL KOLKATA	NORTH 	ARCHITECTS: ABIN DESIGN STUDIO ARCHITECTURE INTERIOR DESIGN GRAPHICS INDUSTRIAL DESIGN 74 G, BONDEL ROAD, GROUND FLOOR, KOLKATA - 700 019
	CHECKED			CONCEPT			
	DATE	12.10.07		APPROVAL			
	FILENAME			PRELIMINARY			
	D:\SOUTH CITY SCHOOL PLUMBING AND FIREWORKER OF DWG.			TENDER			
SCALE :- AS SHOWN				INFORMATION ONLY			
DRAWING NO.: A-2.05/ IT- 21				CONSTRUCTION			
				AS-BUILT			

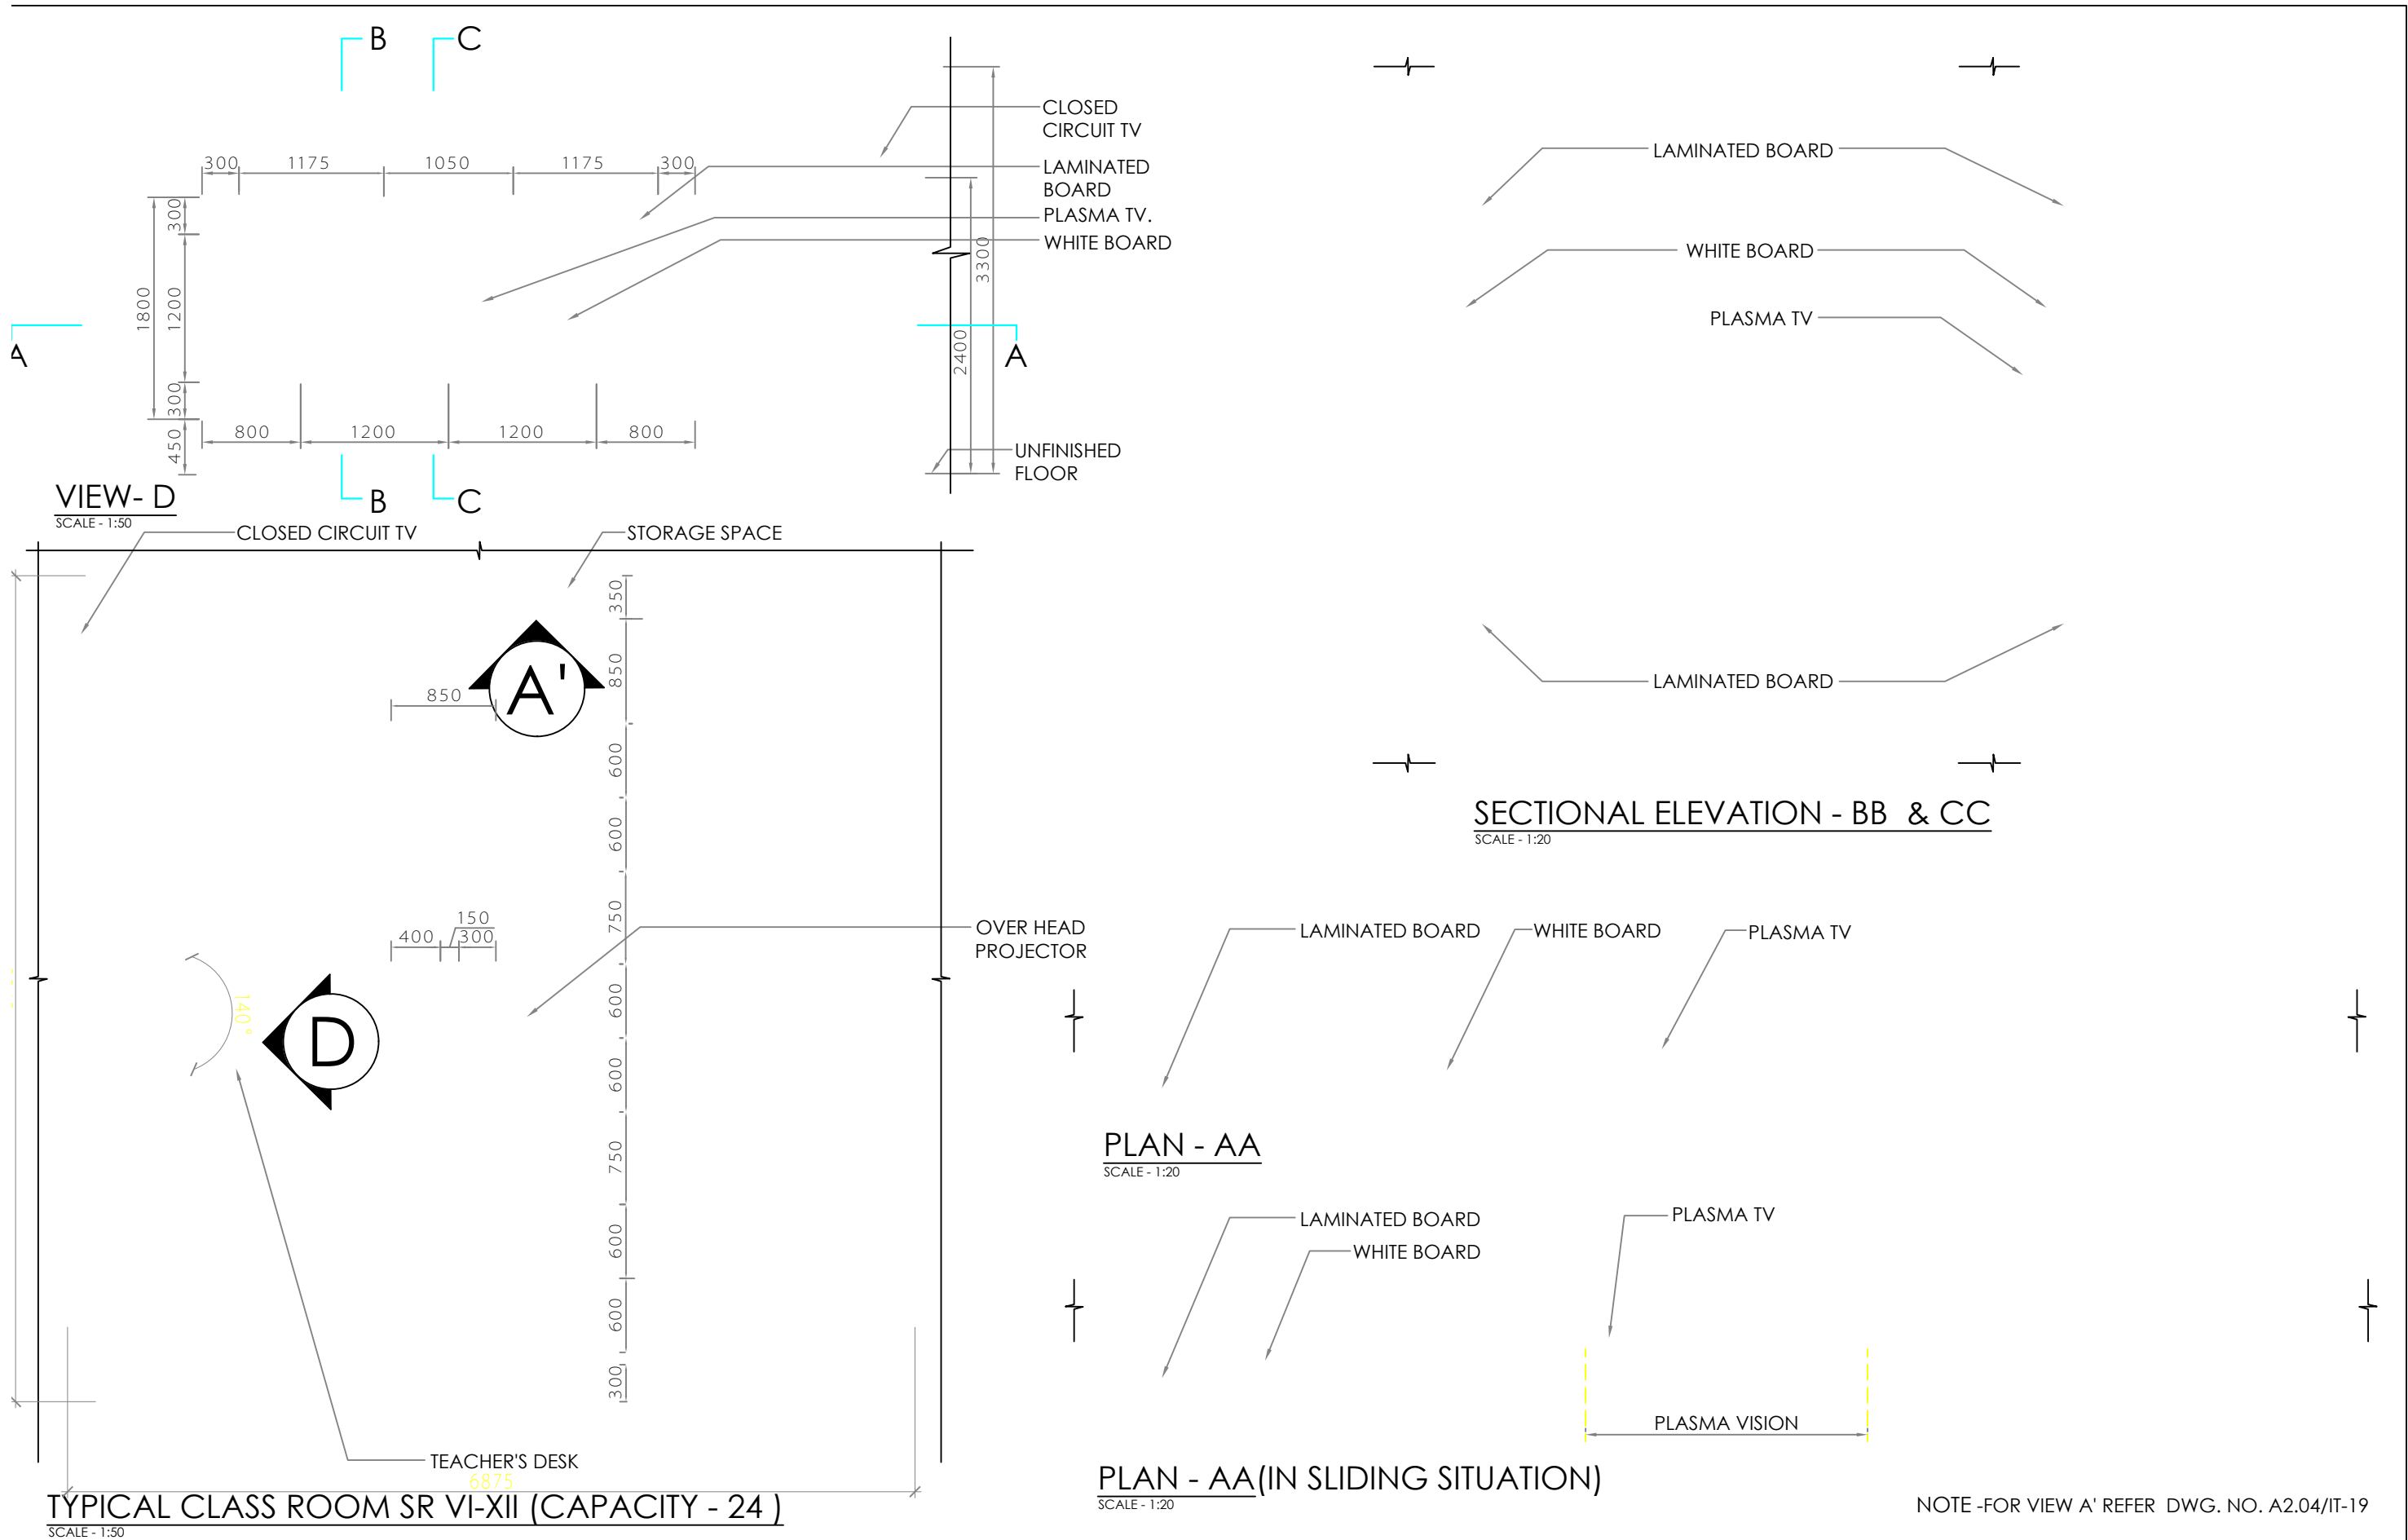


NOTES THIS DRAWING IS THE PROPERTY OF ABIN DESIGN STUDIO AND CANNOT BE COPIED, CIRCULATED OR USED IN ANY MANNER OTHER THAN THE PURPOSE FOR WHICH IT IS ISSUED WITHOUT THEIR WRITTEN PERMISSION WORK TO FIGURED DIMENSIONS ONLY ALL DIMENSIONS ARE TO ROUGH SURFACES OR CENTRE LINES AND DO NOT INCLUDE FINISHES UNLESS NOTED OTHERWISE ANY DISCREPANCY IN DIMENSIONS OR BETWEEN THIS DRAWING & ANY OTHER MUST BE BROUGHT TO ARCHITECT'S IMMEDIATE NOTICE ALL DIMENSIONS ARE IN MILLIMETERS	DRAWN	RELEASED FOR	TITLE:	NORTH 	ARCHITECTS: ABIN DESIGN STUDIO ARCHITECTURE INTERIOR DESIGN GRAPHICS INDUSTRIAL DESIGN 74 G. BONDEL ROAD, GROUND FLOOR, KOLKATA - 700 019
	CHECKED	CONCEPT	INTERIOR LAYOUT		
	DATE	APPROVAL			
	FILENAME	PRELIMINARY	PROJECT:		
	SCALE :- AS SHOWN	TENDER	SOUTH CITY INTERNATIONAL SCHOOL		
	DRAWING NO.: A-2.05/ IT- 22	INFORMATION ONLY	KOLKATA		
		CONSTRUCTION			
		AS-BUILT			

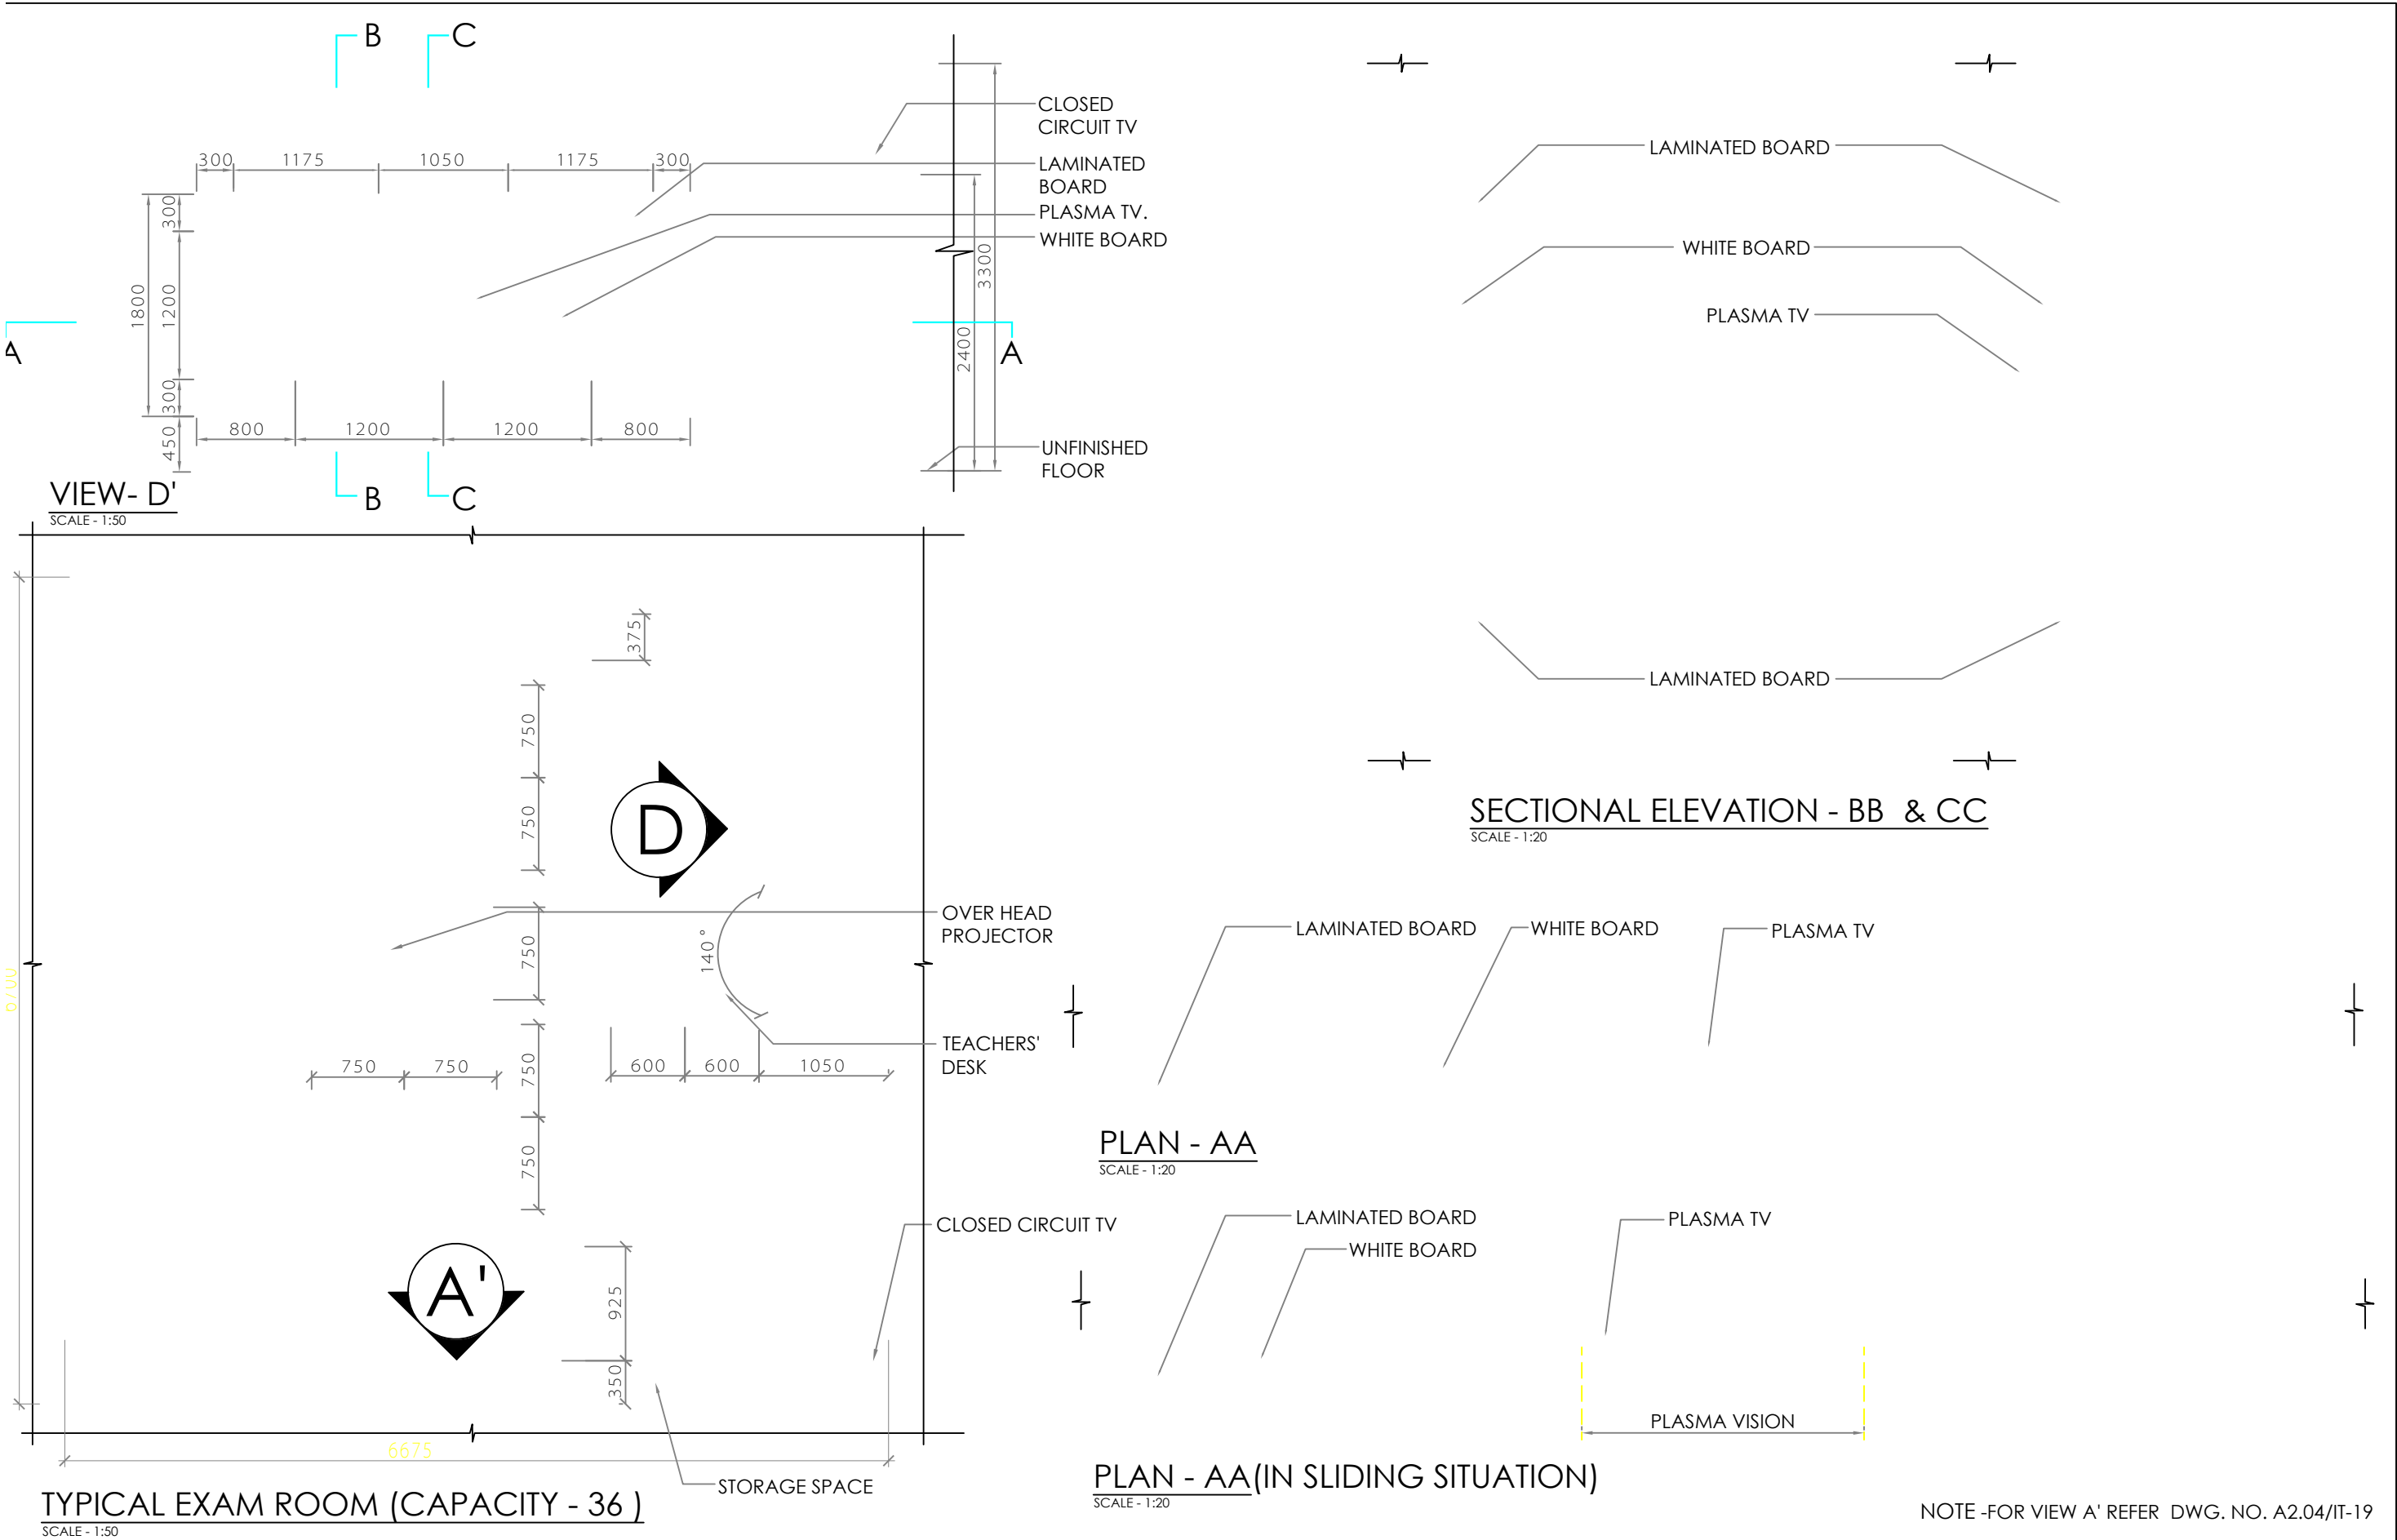

NOTES 1. THIS DRAWING IS THE PROPERTY OF ABIN DESIGN STUDIO AND CANNOT BE COPIED, CIRCULATED OR USED IN ANY MANNER OTHER THAN THE PURPOSE FOR WHICH IT IS ISSUED WITHOUT THEIR WRITTEN PERMISSION 2. WORK TO FIGURED DIMENSIONS ONLY 3. ALL DIMENSIONS ARE TO ROUGH SURFACES OR CENTRE LINES AND DO NOT INCLUDE FINISHES UNLESS NOTED OTHERWISE 4. ANY DISCREPANCY IN DIMENSIONS OR BETWEEN THIS DRAWING & ANY OTHER MUST BE BROUGHT TO ARCHITECT'S IMMEDIATE NOTICE 5. ALL DIMENSIONS ARE IN MILLIMETERS	DRAWN		RELEASED FOR	TITLE:	NORTH 	ARCHITECTS: ABIN DESIGN STUDIO ARCHITECTURE INTERIOR DESIGN GRAPHICS INDUSTRIAL DESIGN 74 G, BONDEL ROAD, GROUND FLOOR, KOLKATA - 700 019
	CHECKED		CONCEPT	INTERIOR LAYOUT		
	DATE	12.10.07	APPROVAL			
	FILENAME		PRELIMINARY	PROJECT:		
	D:\SOUTH CITY SCHOOL PLUMBING AND FIREWORK OF DWG.		TENDER	SOUTH CITY INTERNATIONAL SCHOOL		
	SCALE :- AS SHOWN		INFORMATION ONLY	KOLKATA		
	DRAWING NO.:	A-2.05/ IT- 20	CONSTRUCTION			
			AS-BUILT			

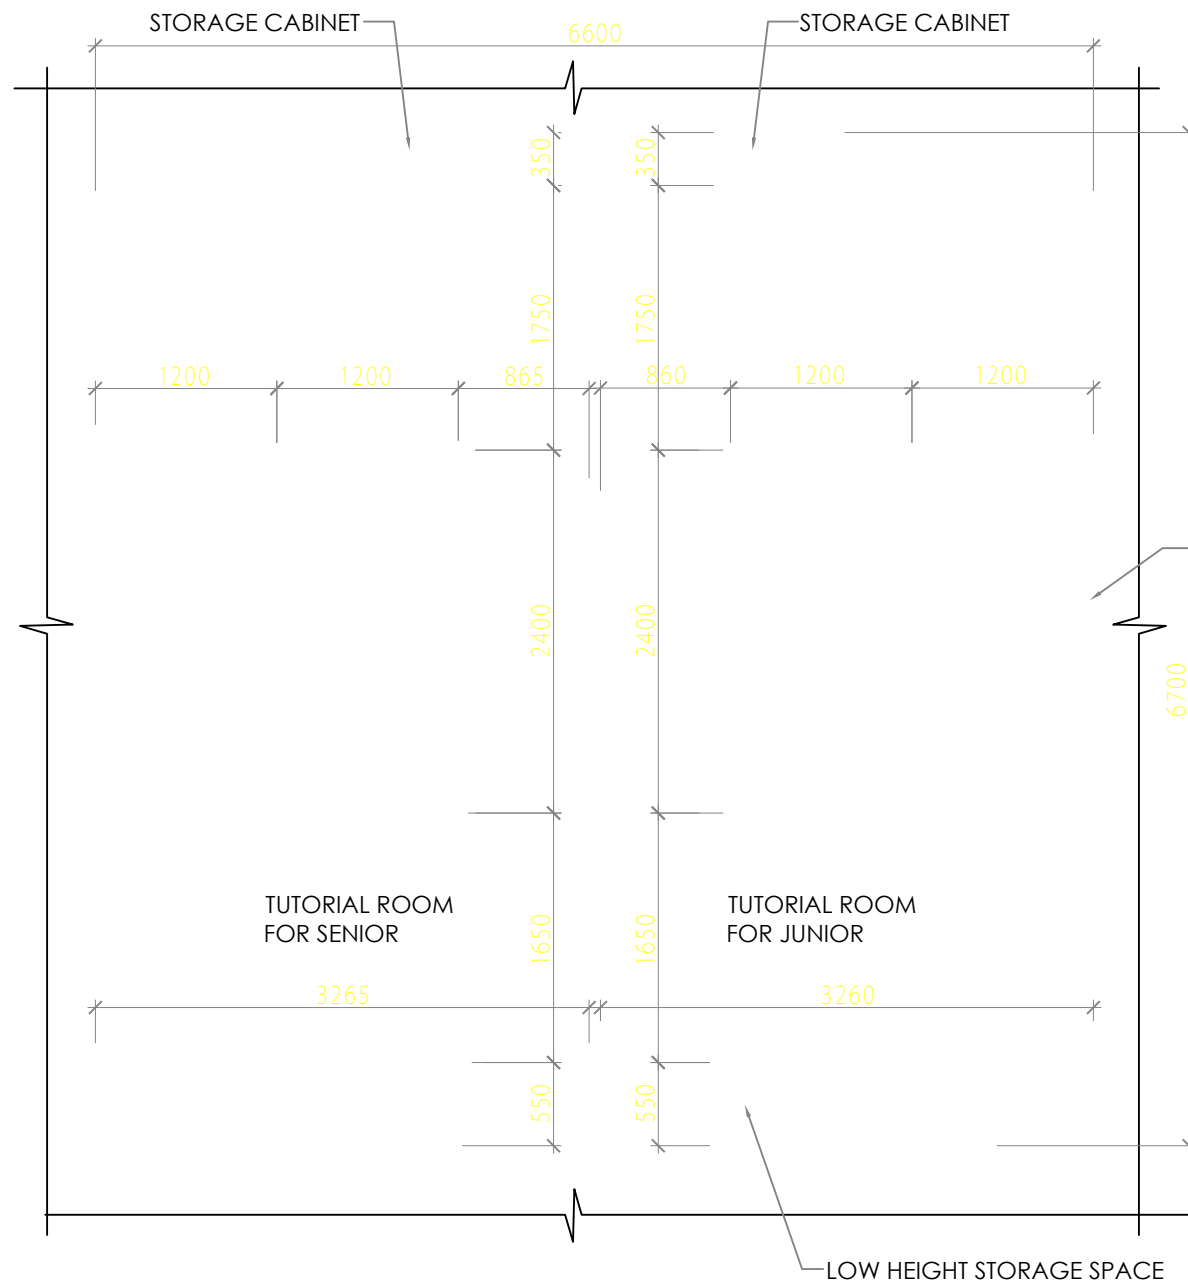

TUTORIAL (CAPACITY - 30)
SCALE - 1:50

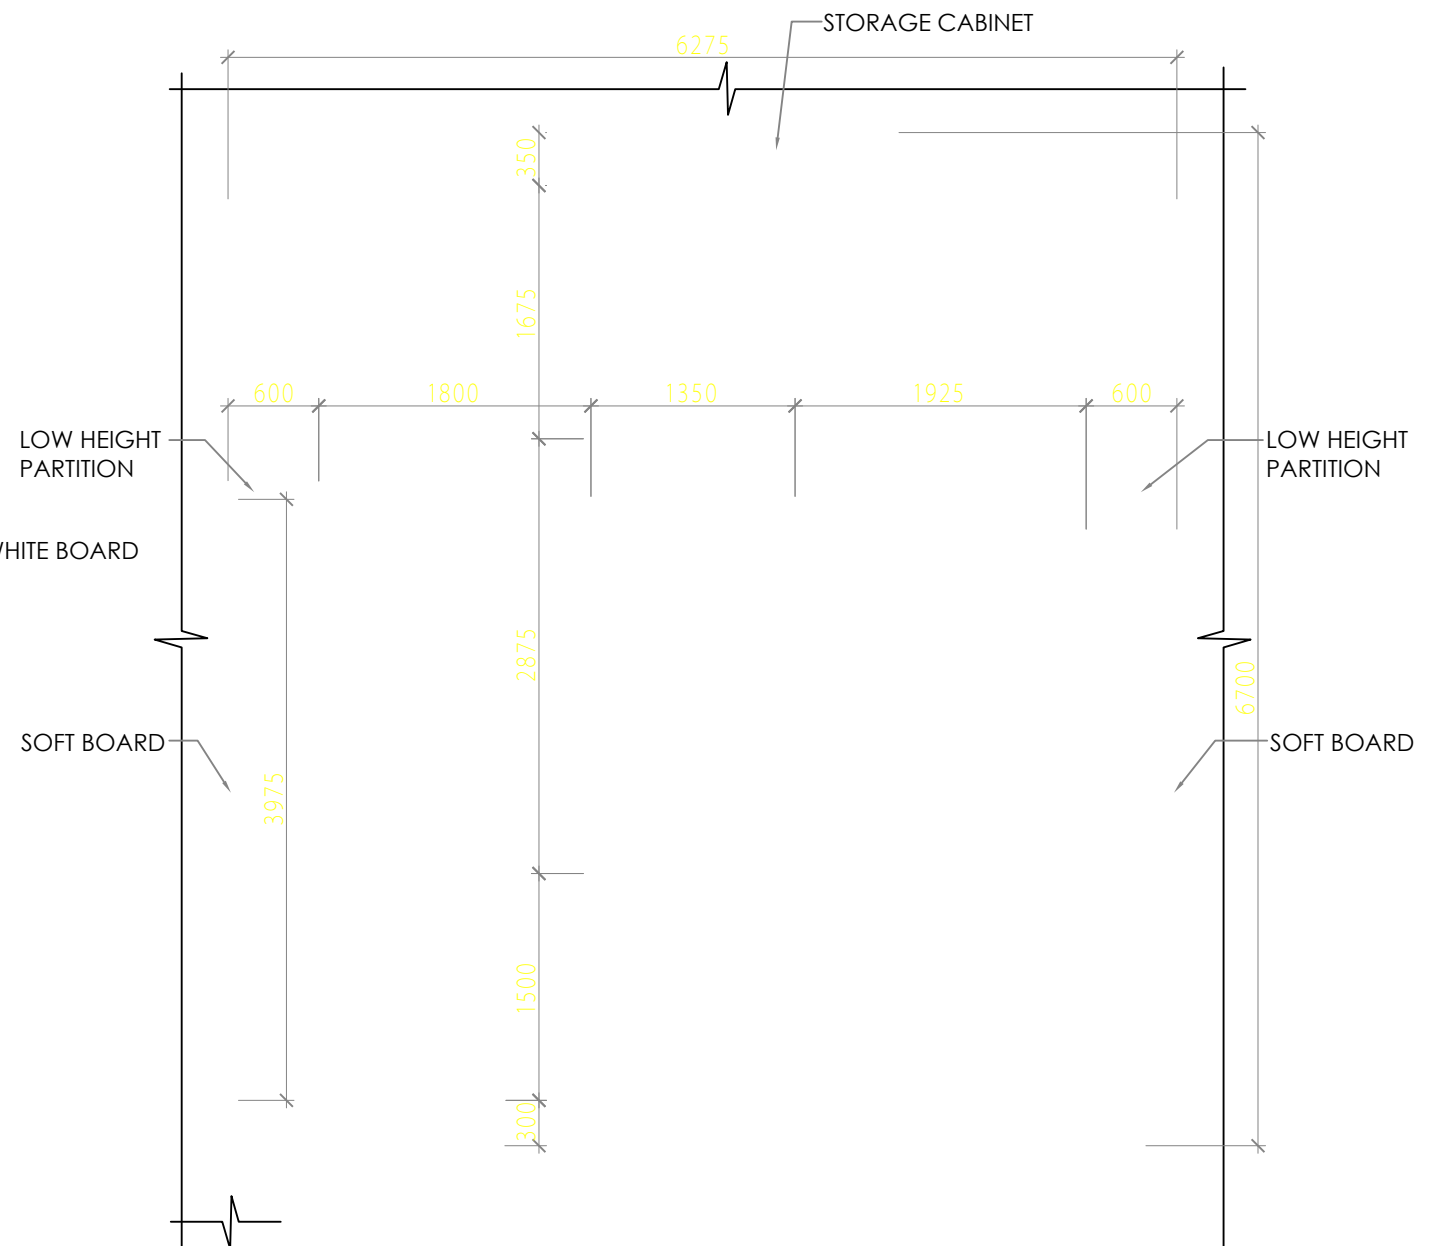

CO-ORDINATORS' OFFICE
SCALE - 1:50

NOTES 1 THIS DRAWING IS THE PROPERTY OF ABIN DESIGN STUDIO AND CANNOT BE COPIED, CIRCULATED OR USED IN ANY MANNER OTHER THAN THE PURPOSE FOR WHICH IT IS ISSUED WITHOUT THEIR WRITTEN PERMISSION 2 WORK TO FIGURED DIMENSIONS ONLY 3 ALL DIMENSIONS ARE TO ROUGH SURFACES OR CENTRE LINES AND DO NOT INCLUDE FINISHES UNLESS NOTED OTHERWISE 4 ANY DISCREPANCY IN DIMENSIONS OR BETWEEN THIS DRAWING & ANY OTHER MUST BE BROUGHT TO ARCHITECT'S IMMEDIATE NOTICE 5 ALL DIMENSIONS ARE IN MILLIMETERS	DRAWN		RELEASED FOR		TITLE: INTERIOR LAYOUT PROJECT: SOUTH CITY INTERNATIONAL SCHOOL KOLKATA	NORTH 	ARCHITECTS: ABIN DESIGN STUDIO ARCHITECTURE INTERIOR DESIGN GRAPHICS INDUSTRIAL DESIGN 74 G, BONDEL ROAD, GROUND FLOOR, KOLKATA - 700 019
	CHECKED		CONCEPT				
	DATE	12.10.07	APPROVAL				
	FILENAME		PRELIMINARY				
	D:\SOUTH CITY SCHOOL\PLUMBING AND FIRE\LOWER GF.DWG		TENDER				
	SCALE :-	AS SHOWN	INFORMATION ONLY				
	DRAWING NO.:	A-2.05/ IT- 23	CONSTRUCTION				
			AS-BUILT				