


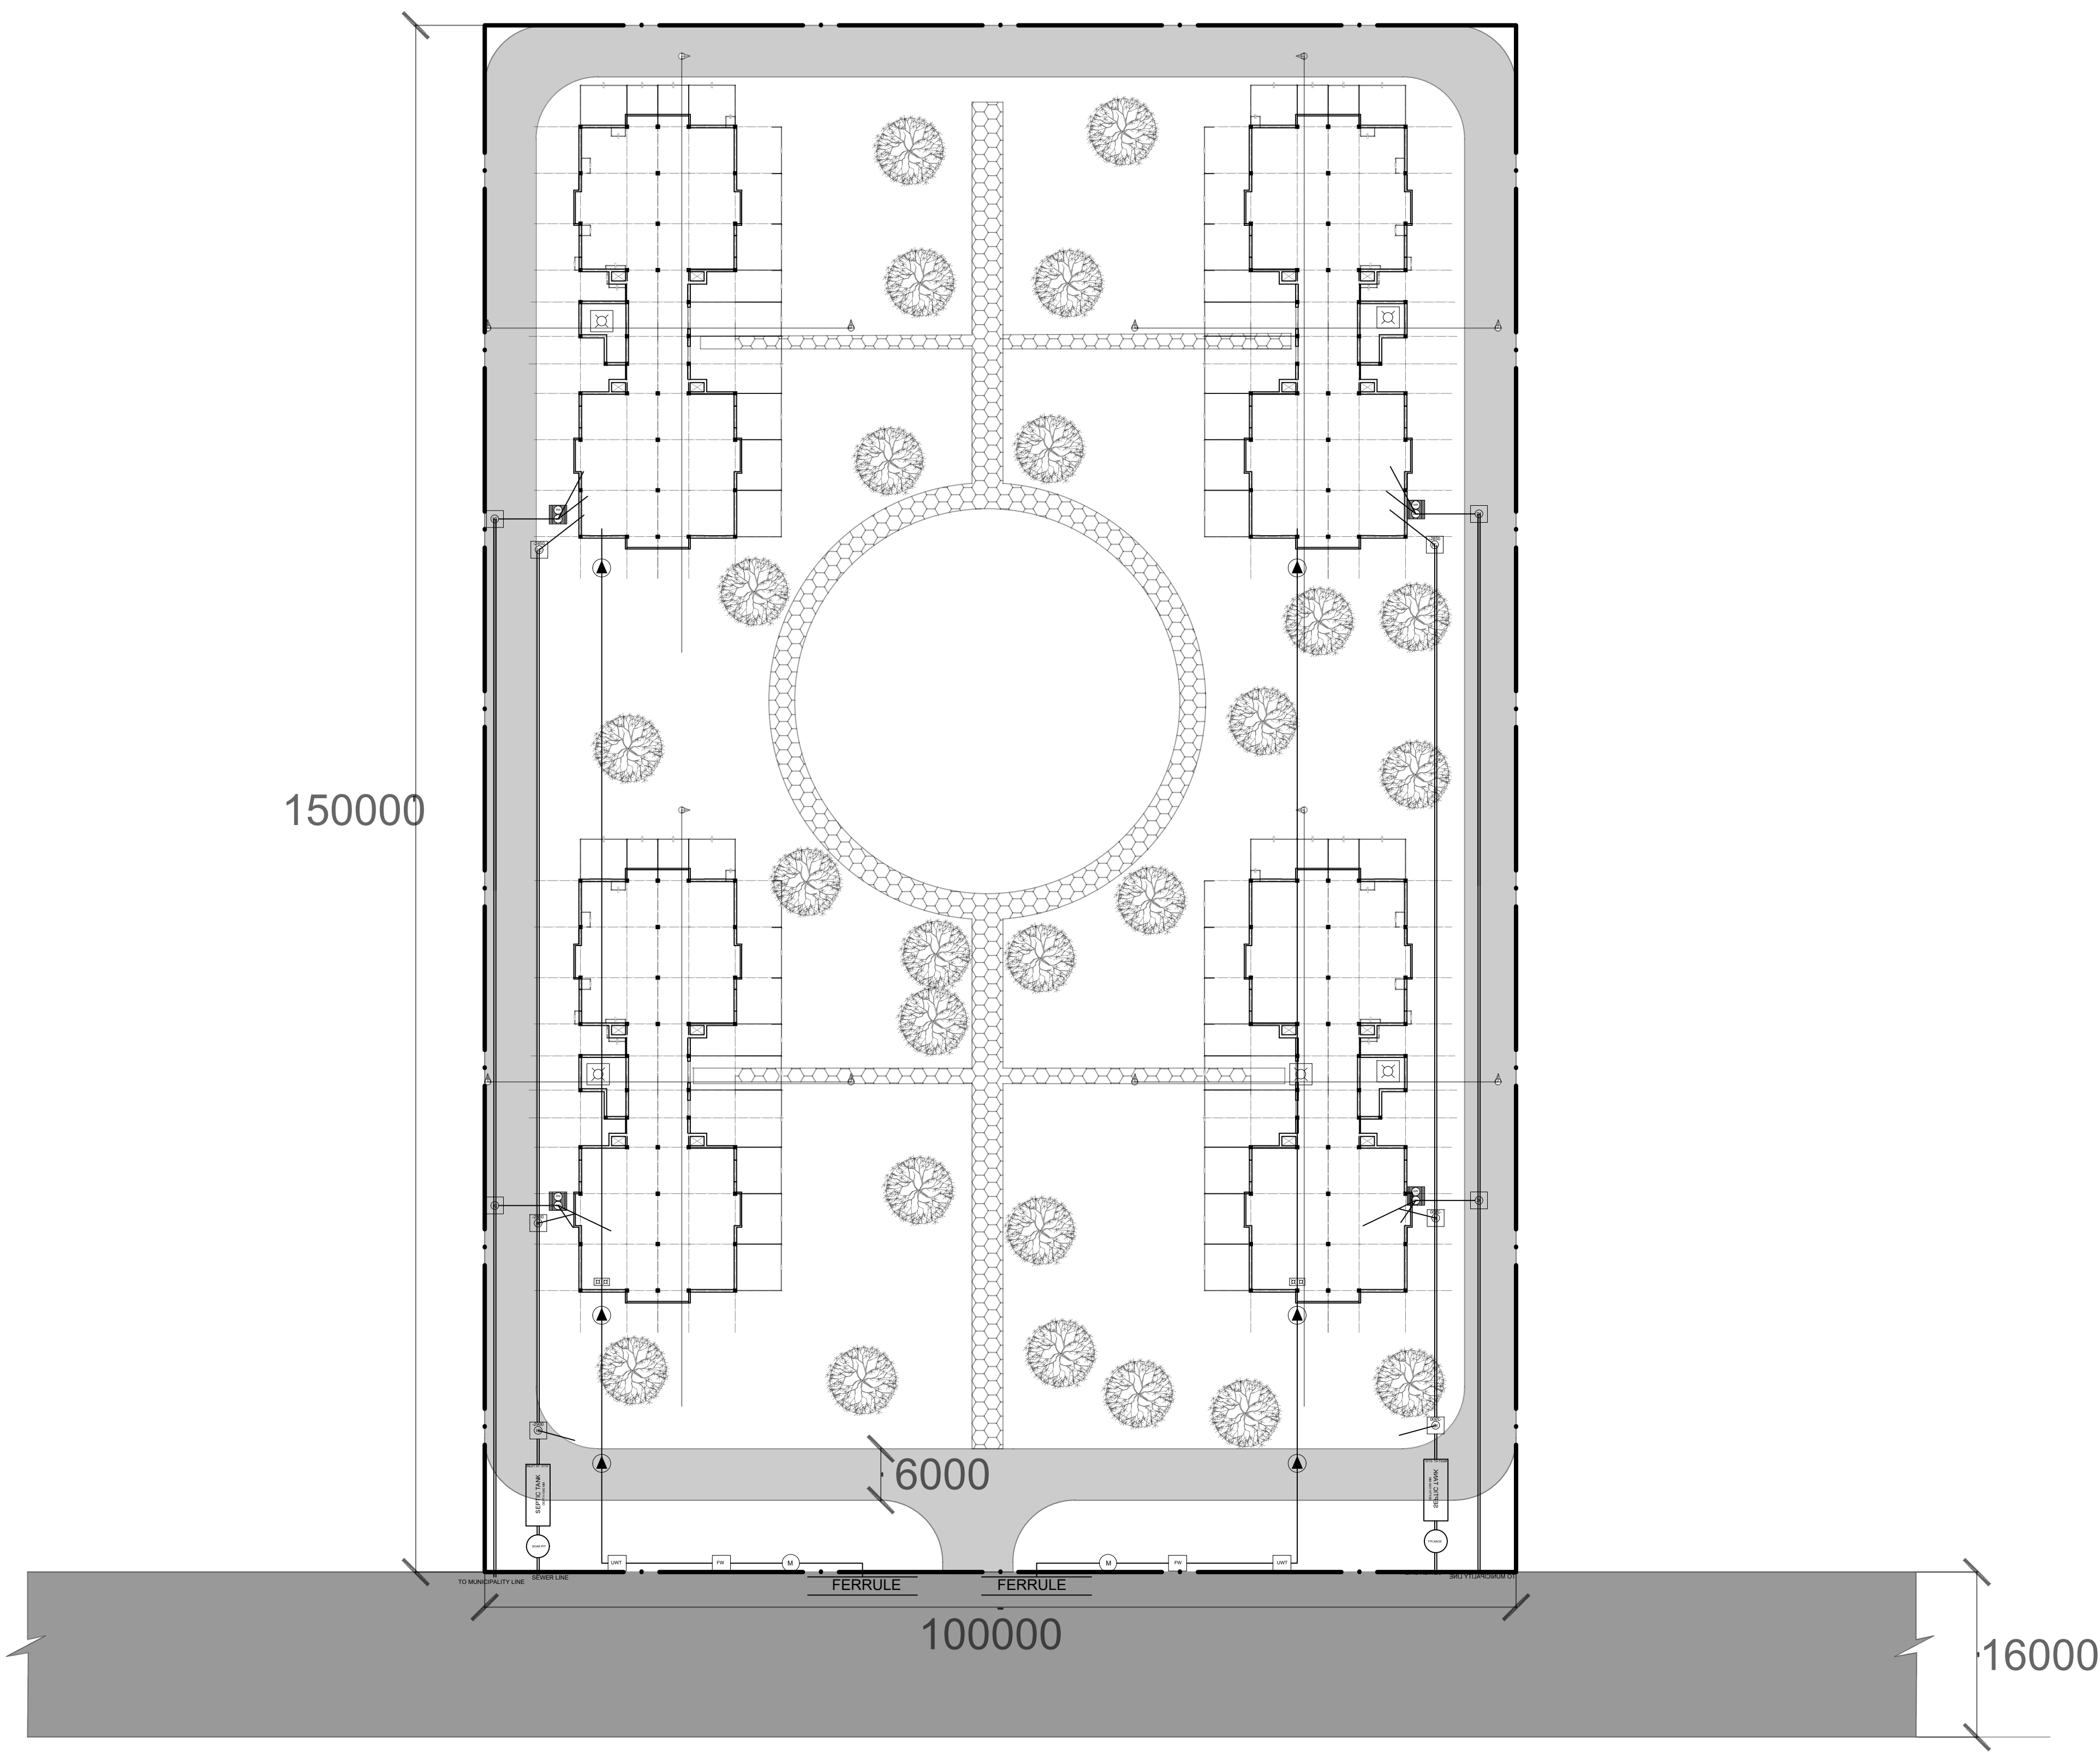

SITE WATER SUPPLY & DRAINAGE

NOTES

ALL DIMENSIONS ARE IN MM UNLESS NOTED OTHERWISE

THE DIMENSIONS ARE TO BE READ AND NOT SCALED OFF THE DRAWING.

ANY DISCREPENCY IN THE DRAWING SHALL BE BROUGHT TO THE NOTICE OF THE ARCHITECTS.

THIS DRAWING IS TO BE READ IN CONJUNCTION WITH OTHER RELEVANT DRAWINGS.

LEGENDS

| SYMBOL | MEANING                |
|--------|------------------------|
|        | Water Meter            |
|        | Fire Water             |
|        | Underground Water Tank |
|        | Pump                   |
|        | 100 mm Rainwater Pipe  |
|        | 100 mm Wastewater Pipe |
|        | 100 mm Soilwater Pipe  |
|        | 100 mm Vent Pipe       |
|        | Gully Trap             |
|        | Inspection Chamber     |
|        | Inspection Trap        |
|        | Overhead Water Tank    |
|        | 200 mm dia pipe        |
|        | STREET LAMP            |

Name: PRAKHAR VERMA  
Roll No: 22AR10017

Working Drawing-I (AR32201)  
Semester: VI  
SPRING-2025

Department of Architecture & Regional Planning  
Indian Institute of Technology  
Kharagpur

Drawing Title

SITE PLAN

Scale -

Dwg no.  
2

Date-  
07/04/2025