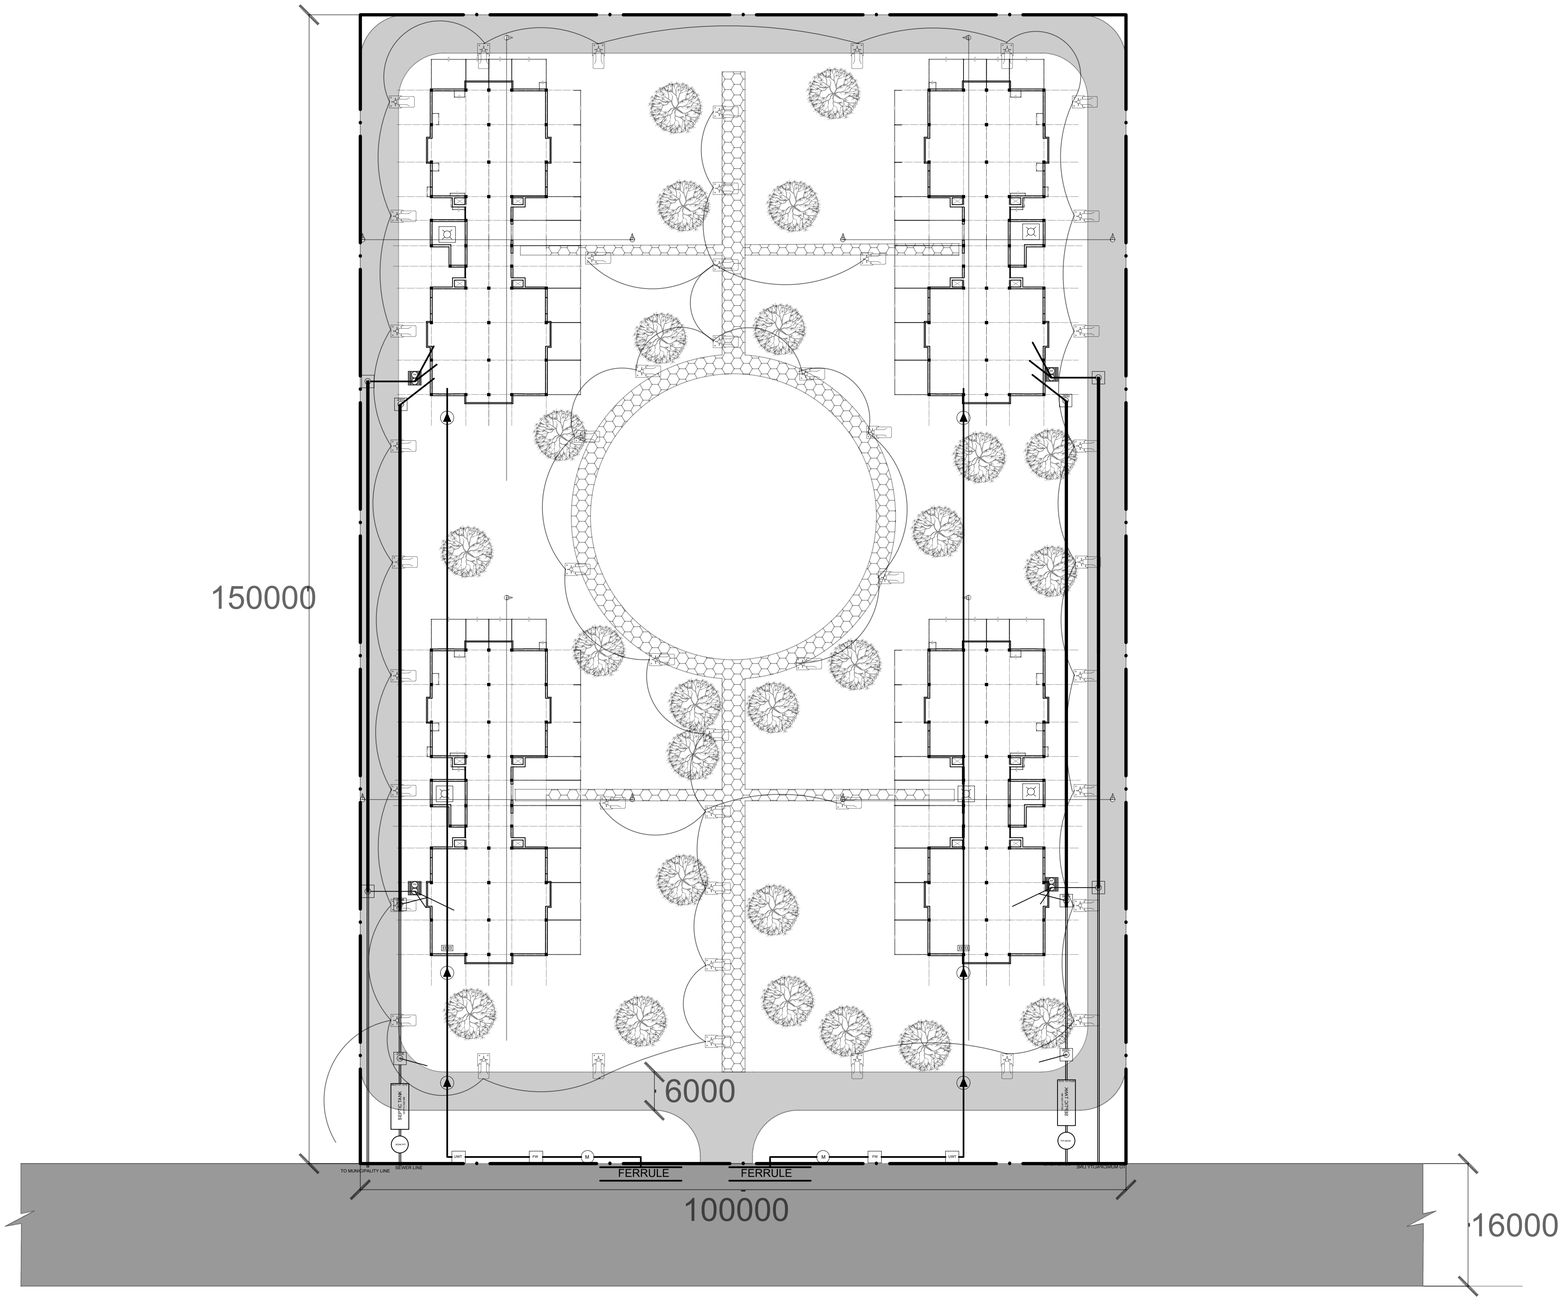


NOTES

ALL DIMENSIONS ARE IN MM UNLESS NOTED OTHERWISE

THE DIMENSIONS ARE TO BE READ AND NOT SCALED OFF THE DRAWING.

ANY DISCREPENCY IN THE DRAWING SHALL BE BROUGHT TO THE NOTICE OF THE ARCHITECTS.

THIS DRAWING IS TO BE READ IN CONJUNCTION WITH OTHER RELEVANT DRAWINGS.

LEGENDS

SYMBOL	MEANING
M	Water Meter
FW	Fire Water
UWT	Underground Water Tank
	Pump
RW	100 mm Rainwater Pipe
WW	100 mm Wastewater Pipe
SW	100 mm Soilwater Pipe
VP	100 mm Vent Pipe
	Gully Trap
	Inspection Chamber
	Inspection Trap
	Overhead Water Tank
	200 mm dia pipe
	STREET LAMP

Name: PRAKHAR VERMA
Roll No: 22AR10017

Working Drawing-I (AR32201)
Semester: VI
SPRING-2025

Department of Architecture & Regional Planning
Indian Institute of Technology
Kharagpur

Drawing Title

SITE PLAN

Scale - 1:400

Dwg no. 2

Date- 07/04/2025