


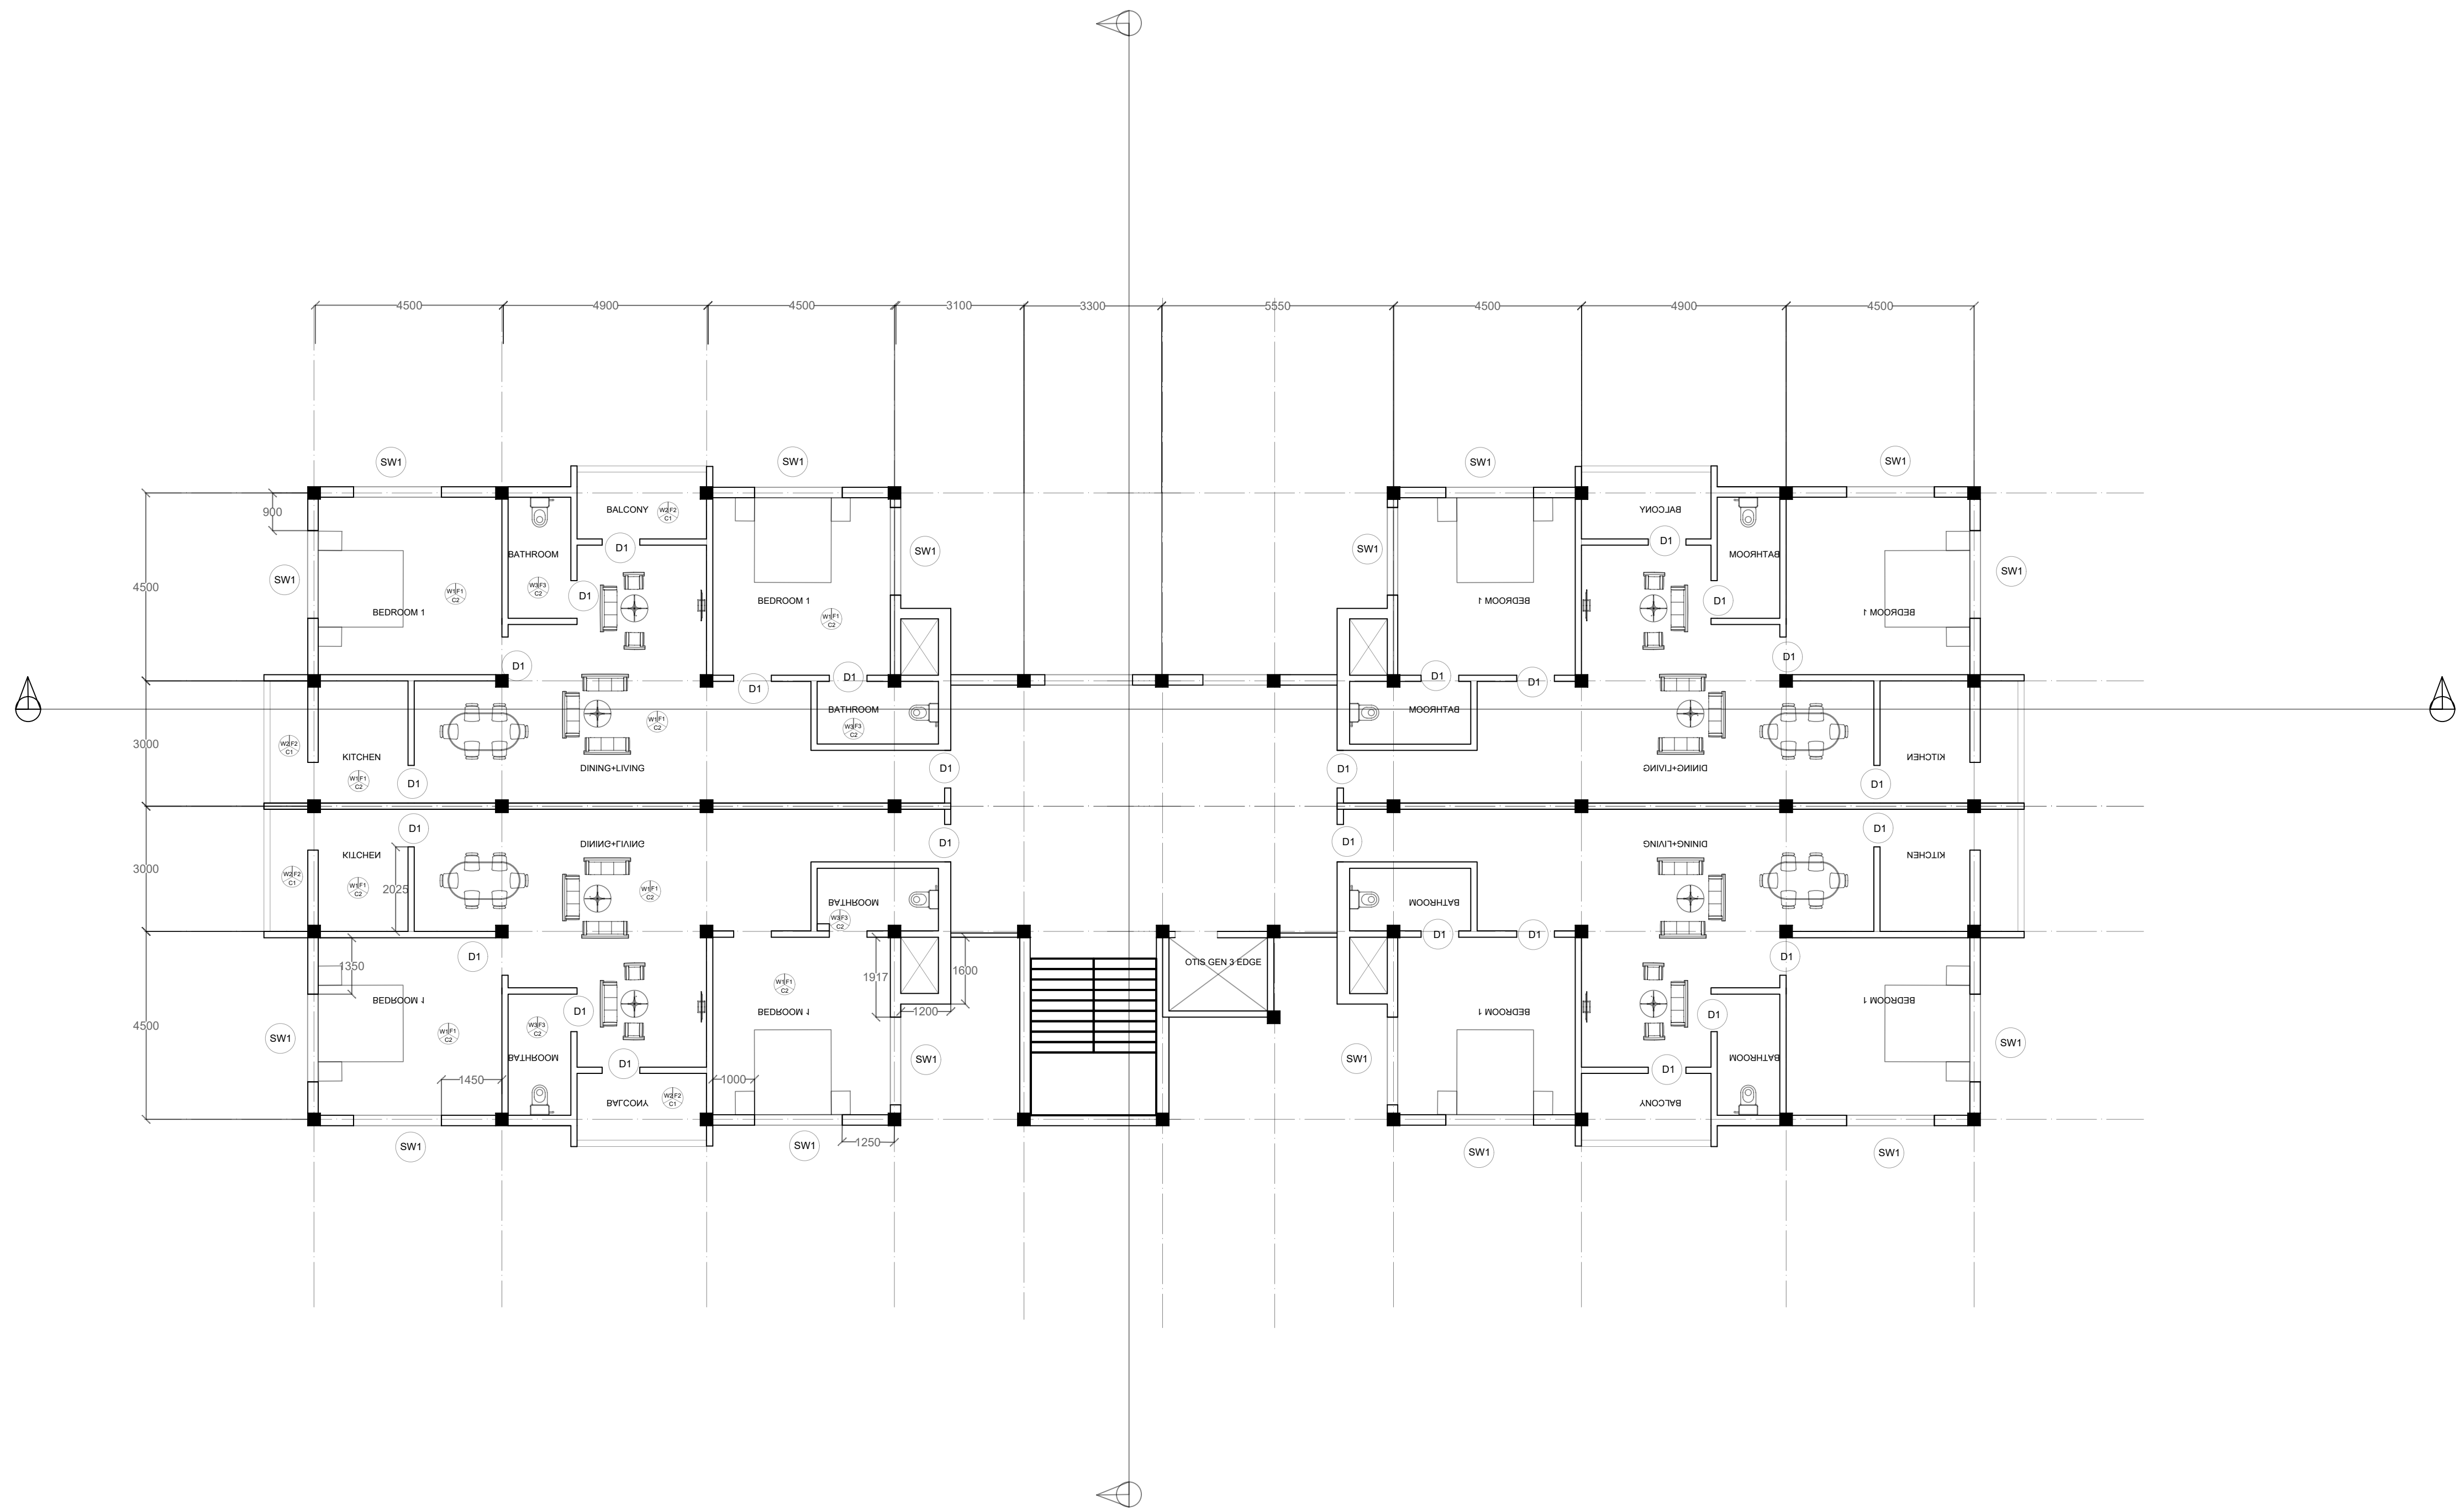

NOTES

ALL DIMENSIONS ARE IN MM UNLESS NOTED OTHERWISE

THE DIMENSIONS ARE TO BE READ AND NOT SCALED OFF THE DRAWING.

ANY DISCREPANCY IN THE DRAWING SHALL BE BROUGHT TO THE NOTICE OF THE ARCHITECTS.

THIS DRAWING IS TO BE READ IN CONJUNCTION WITH OTHER RELEVANT DRAWINGS.

FINISH SCHEDULE		
S. NO.	INDEX	DESCRIPTION
1	W1	PUTTY WITH DISTEMPER PAINT
2	W2	POP WITH DISTEMPER PAINT
3	W3	PUTTY WITH WHITE WASH
4	F1	VITRIFIED TILES
5	F2	MARBLE
6	F3	ANTI SKID CERAMIC TILES
7	F4	POLISHED CONCRETE
8	F5	PORCELAIN TILES
9	C1	POP WITH EMULSION PAINT
10	C2	PUTTY WITH EMULSION PAINT

DOORS AND WINDOW SCHEDULE						
S.No.	INDEX	ITEM	SILL	LINTEL	HEIGHT	MATERIAL
1	D1	DOUBLE DOOR	0	2100	2100	WOOD
2	D2	DOOR	0	2100	2100	WOOD
3	SW1	WINDOW	900	2100	1200	STEEL
4	V1	VENTILATOR	1800	2200	400	-

Name: PRAKHAR VERMA
Roll No: 22AR10017

Working Drawing-I (AR32201)
Semester: VI
SPRING-2025

Department of Architecture & Regional Planning
Indian Institute of Technology
Kharagpur

Drawing Title

TYPICAL FLOOR PLAN

Scale -
1:100

Dwg no.
2

Date-
07/04/2025